
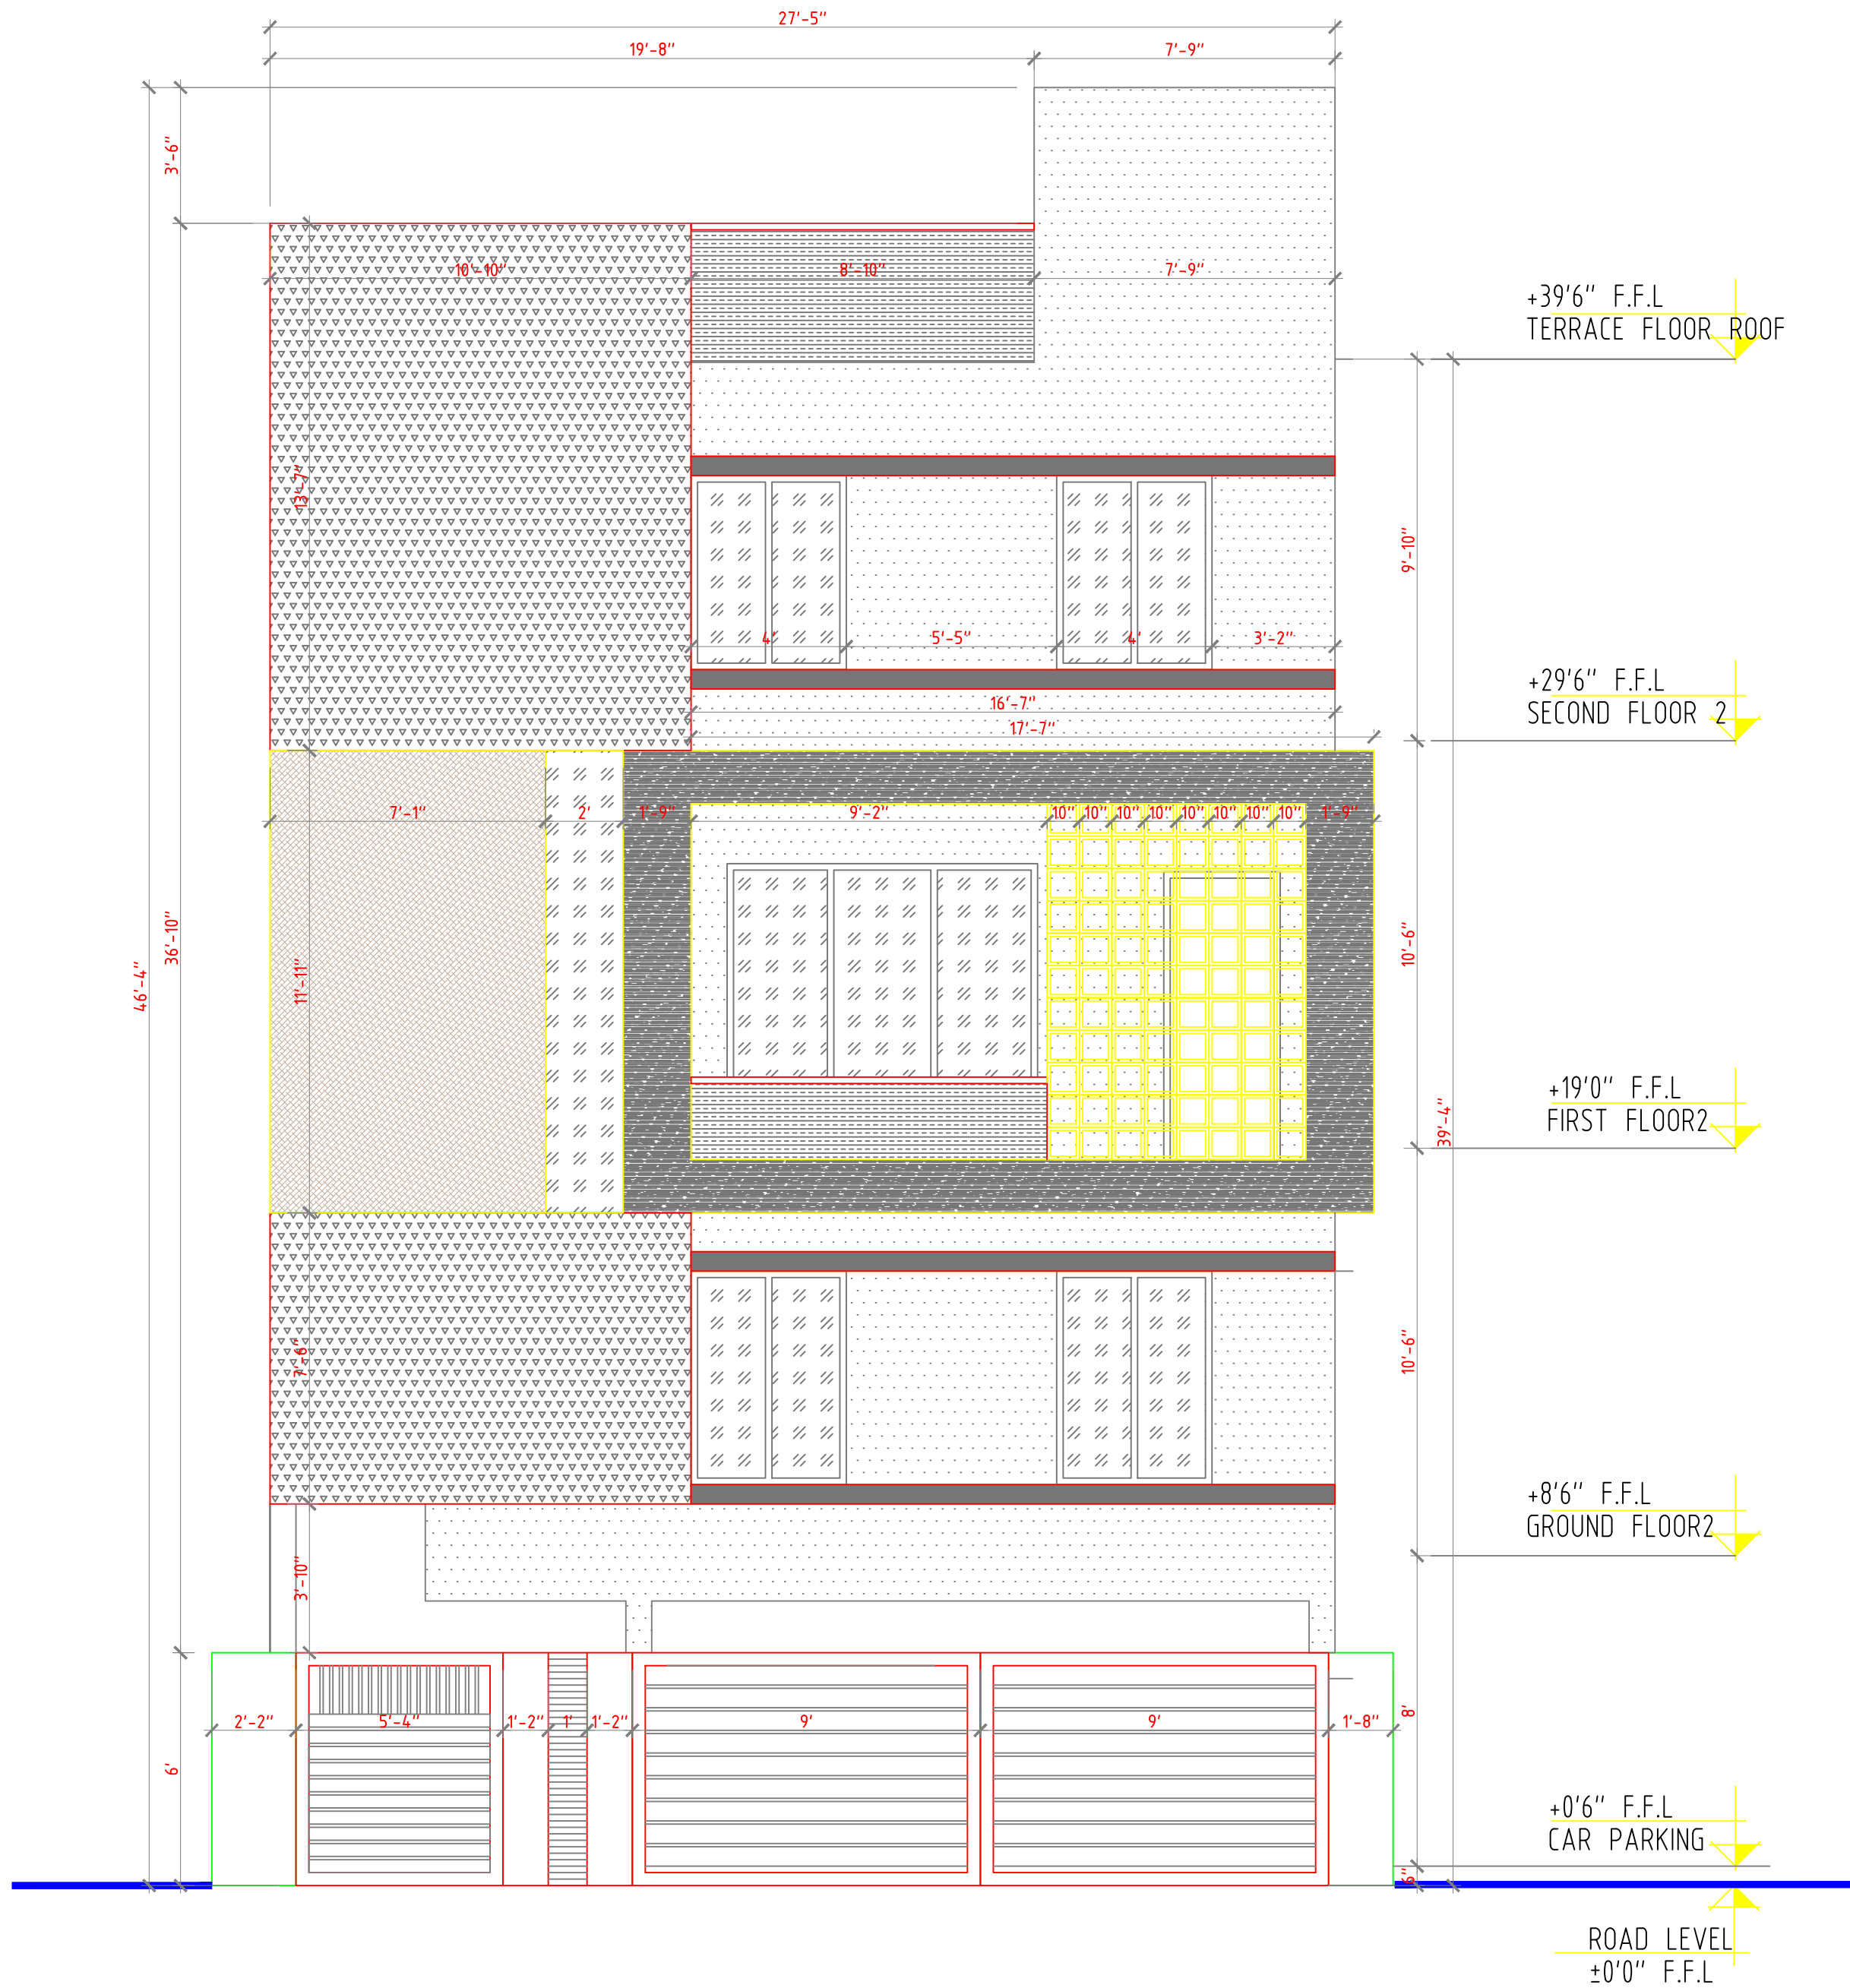


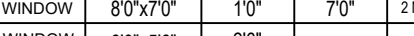

PROJECTS DETAILS :-		CLIENT DETAILS :-		AREA STATEMENT :-		PROJECT TITLE :-		DATE OF SUBMISSION :-		NORTH :-		FROM THE LEGAL TEAM		PARTNER ARCHITECTS :-		OPENING SCHEDULE					Design By :-	
Proposed Residential Villa G+2.	Mr. Narayan			FRONT ELEVATION	07/06/2026			THE ABOVE DRAWING IS THE SOLE PROPERTY OF THE ARCHITECTS AND SHOULD NOT BE PUBLISHED OR USED OTHER WISE WITHOUT THE PRIOR CONSENT OF THE ARCHITECTS.	DSIGN CREW LLP	POWERED THROUGH :- 	DT/01	DOOR	3'6"x8'0"	FFL	7'0"	1 NOS						
	SITE ADDRESS :-				REVISION NUMBER :-						SCALE :-		DT/02	DOOR	3'0"x8'0"	FFL		7'0"	7 NOS			
	Prestige Great Acres				R No. R2						1:100		DT/03	DOOR	2'6"x8'0"	FFL		7'0"	6 NOS			
													BD/01	DOOR	2'6"x8'0"	FFL		7'0"	2 NOS			
								WA-01	WINDOW	8'0"x7'0"	1'0"	7'0"	2 NOS									
								WA-02	WINDOW	6'0"x5'6"	2'6"	7'0"	7 NOS									
								WA-03	WINDOW	4'0"x5'6"	2'6"	7'0"	8 NOS									
								VA-01	VENTILATOR	2'0"x2'0"	6'0"	7'0"	7 NOS									