
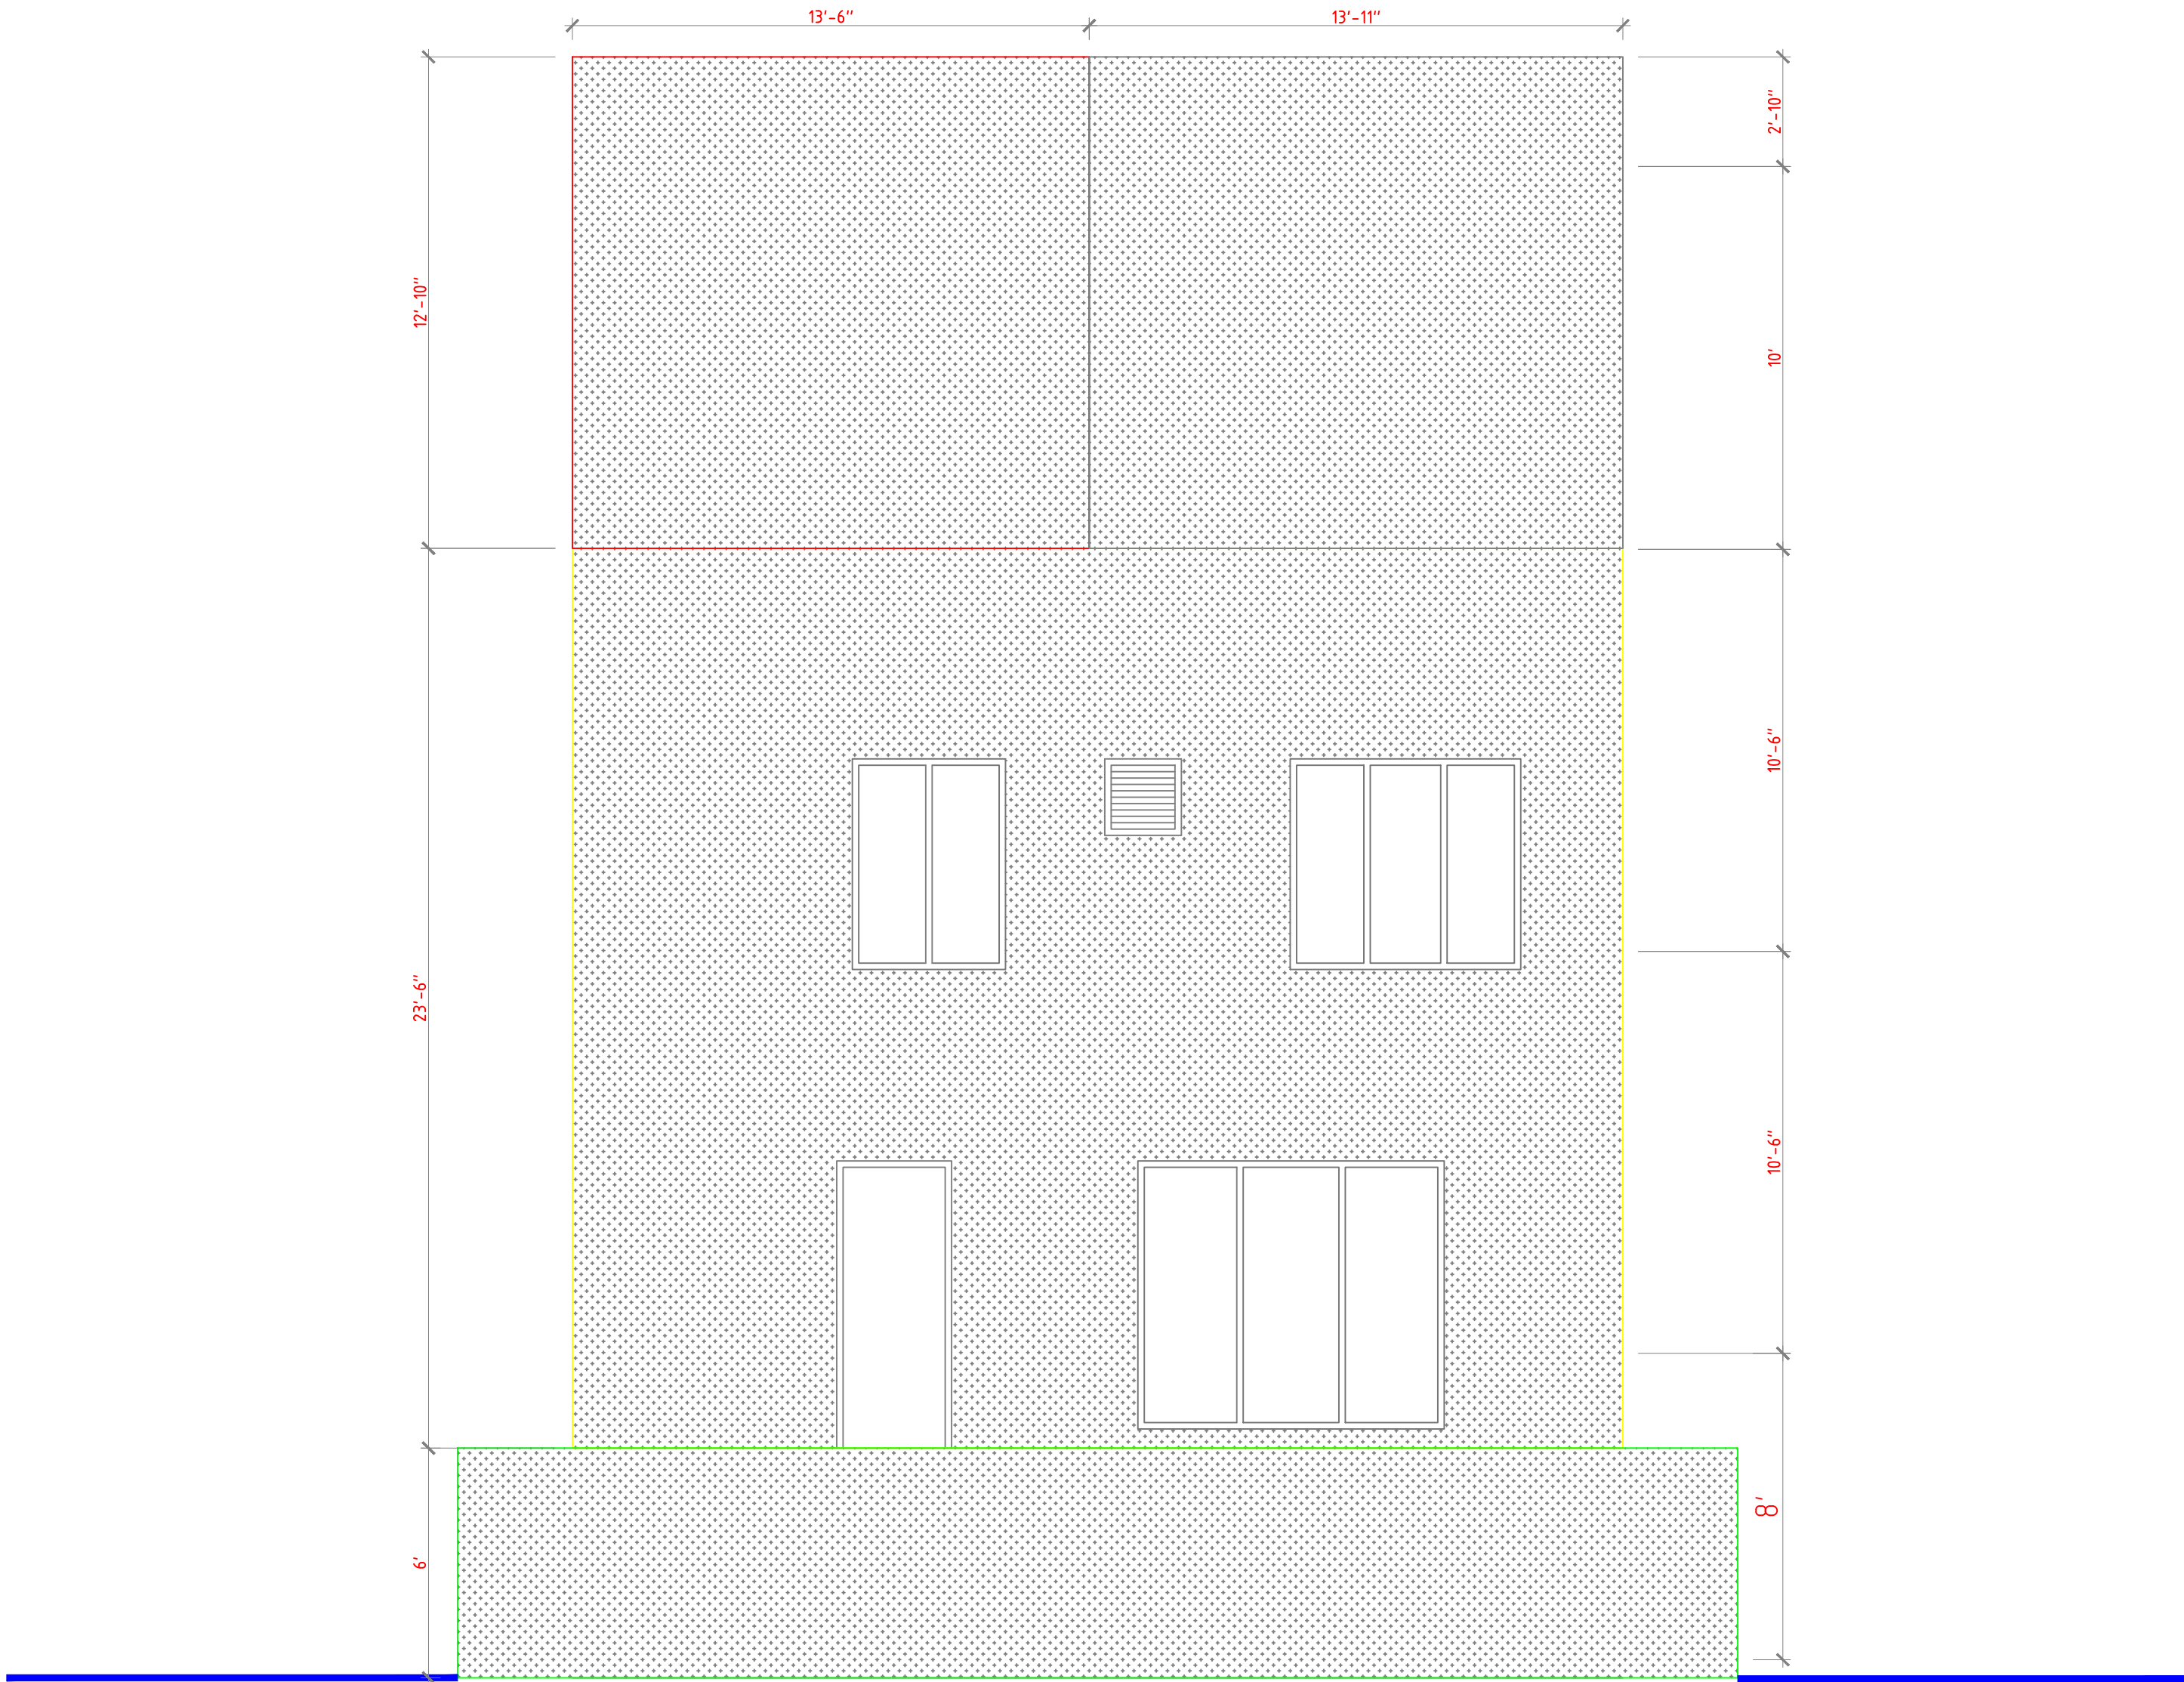


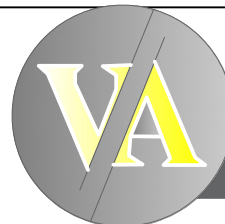

PROJECTS DETAILS :-		CLIENT DETAILS :-		AREA STATEMENT :-		PROJECT TITLE :-		DATE OF SUBMISSION :-		NORTH :-		FROM THE LEGAL TEAM		PARTNER ARCHITECTS :-		OPENING SCHEDULE					Design By :-	
Proposed Residential Villa G+2.		Mr. Narayan				EAST SIDE ELEVATION		07/06/2026				THE ABOVE DRAWING IS THE SOLE PROPERTY OF THE ARCHITECTS AND SHOULD NOT BE PUBLISHED OR USED OTHER WISE WITHOUT THE PRIOR CONSENT OF THE ARCHITECTS.		DSIGN CREW LLP							 AR.VIVEKANANDAN D.arch VISHAL ARCHITECTS Architects and Interiors PH : 6381358459 E-mail- vishalarchitects307@gmail.com	
		SITE ADDRESS :-						REVISION NUMBER :-		SCALE :-						DT/01 DOOR 3'6"x8'0" FFL 7'0" 1 NOS						
		Prestige Great Acres						R No. R2		1:100						DT/02 DOOR 3'0"x8'0" FFL 7'0" 7 NOS						
																DT/03 DOOR 2'6"x8'0" FFL 7'0" 6 NOS						
																BD/01 DOOR 2'6"x8'0" FFL 7'0" 2 NOS						
																WA-01 WINDOW 8'0"x7'0" 1'0" 7'0" 2 NOS						
WA-02 WINDOW 6'0"x5'6" 2'6" 7'0" 7 NOS																						
WA-03 WINDOW 4'0"x5'6" 2'6" 7'0" 8 NOS																						
VA-01 VENTILATOR 2'0"x2'0" 6'0" 7'0" 7 NOS																						