
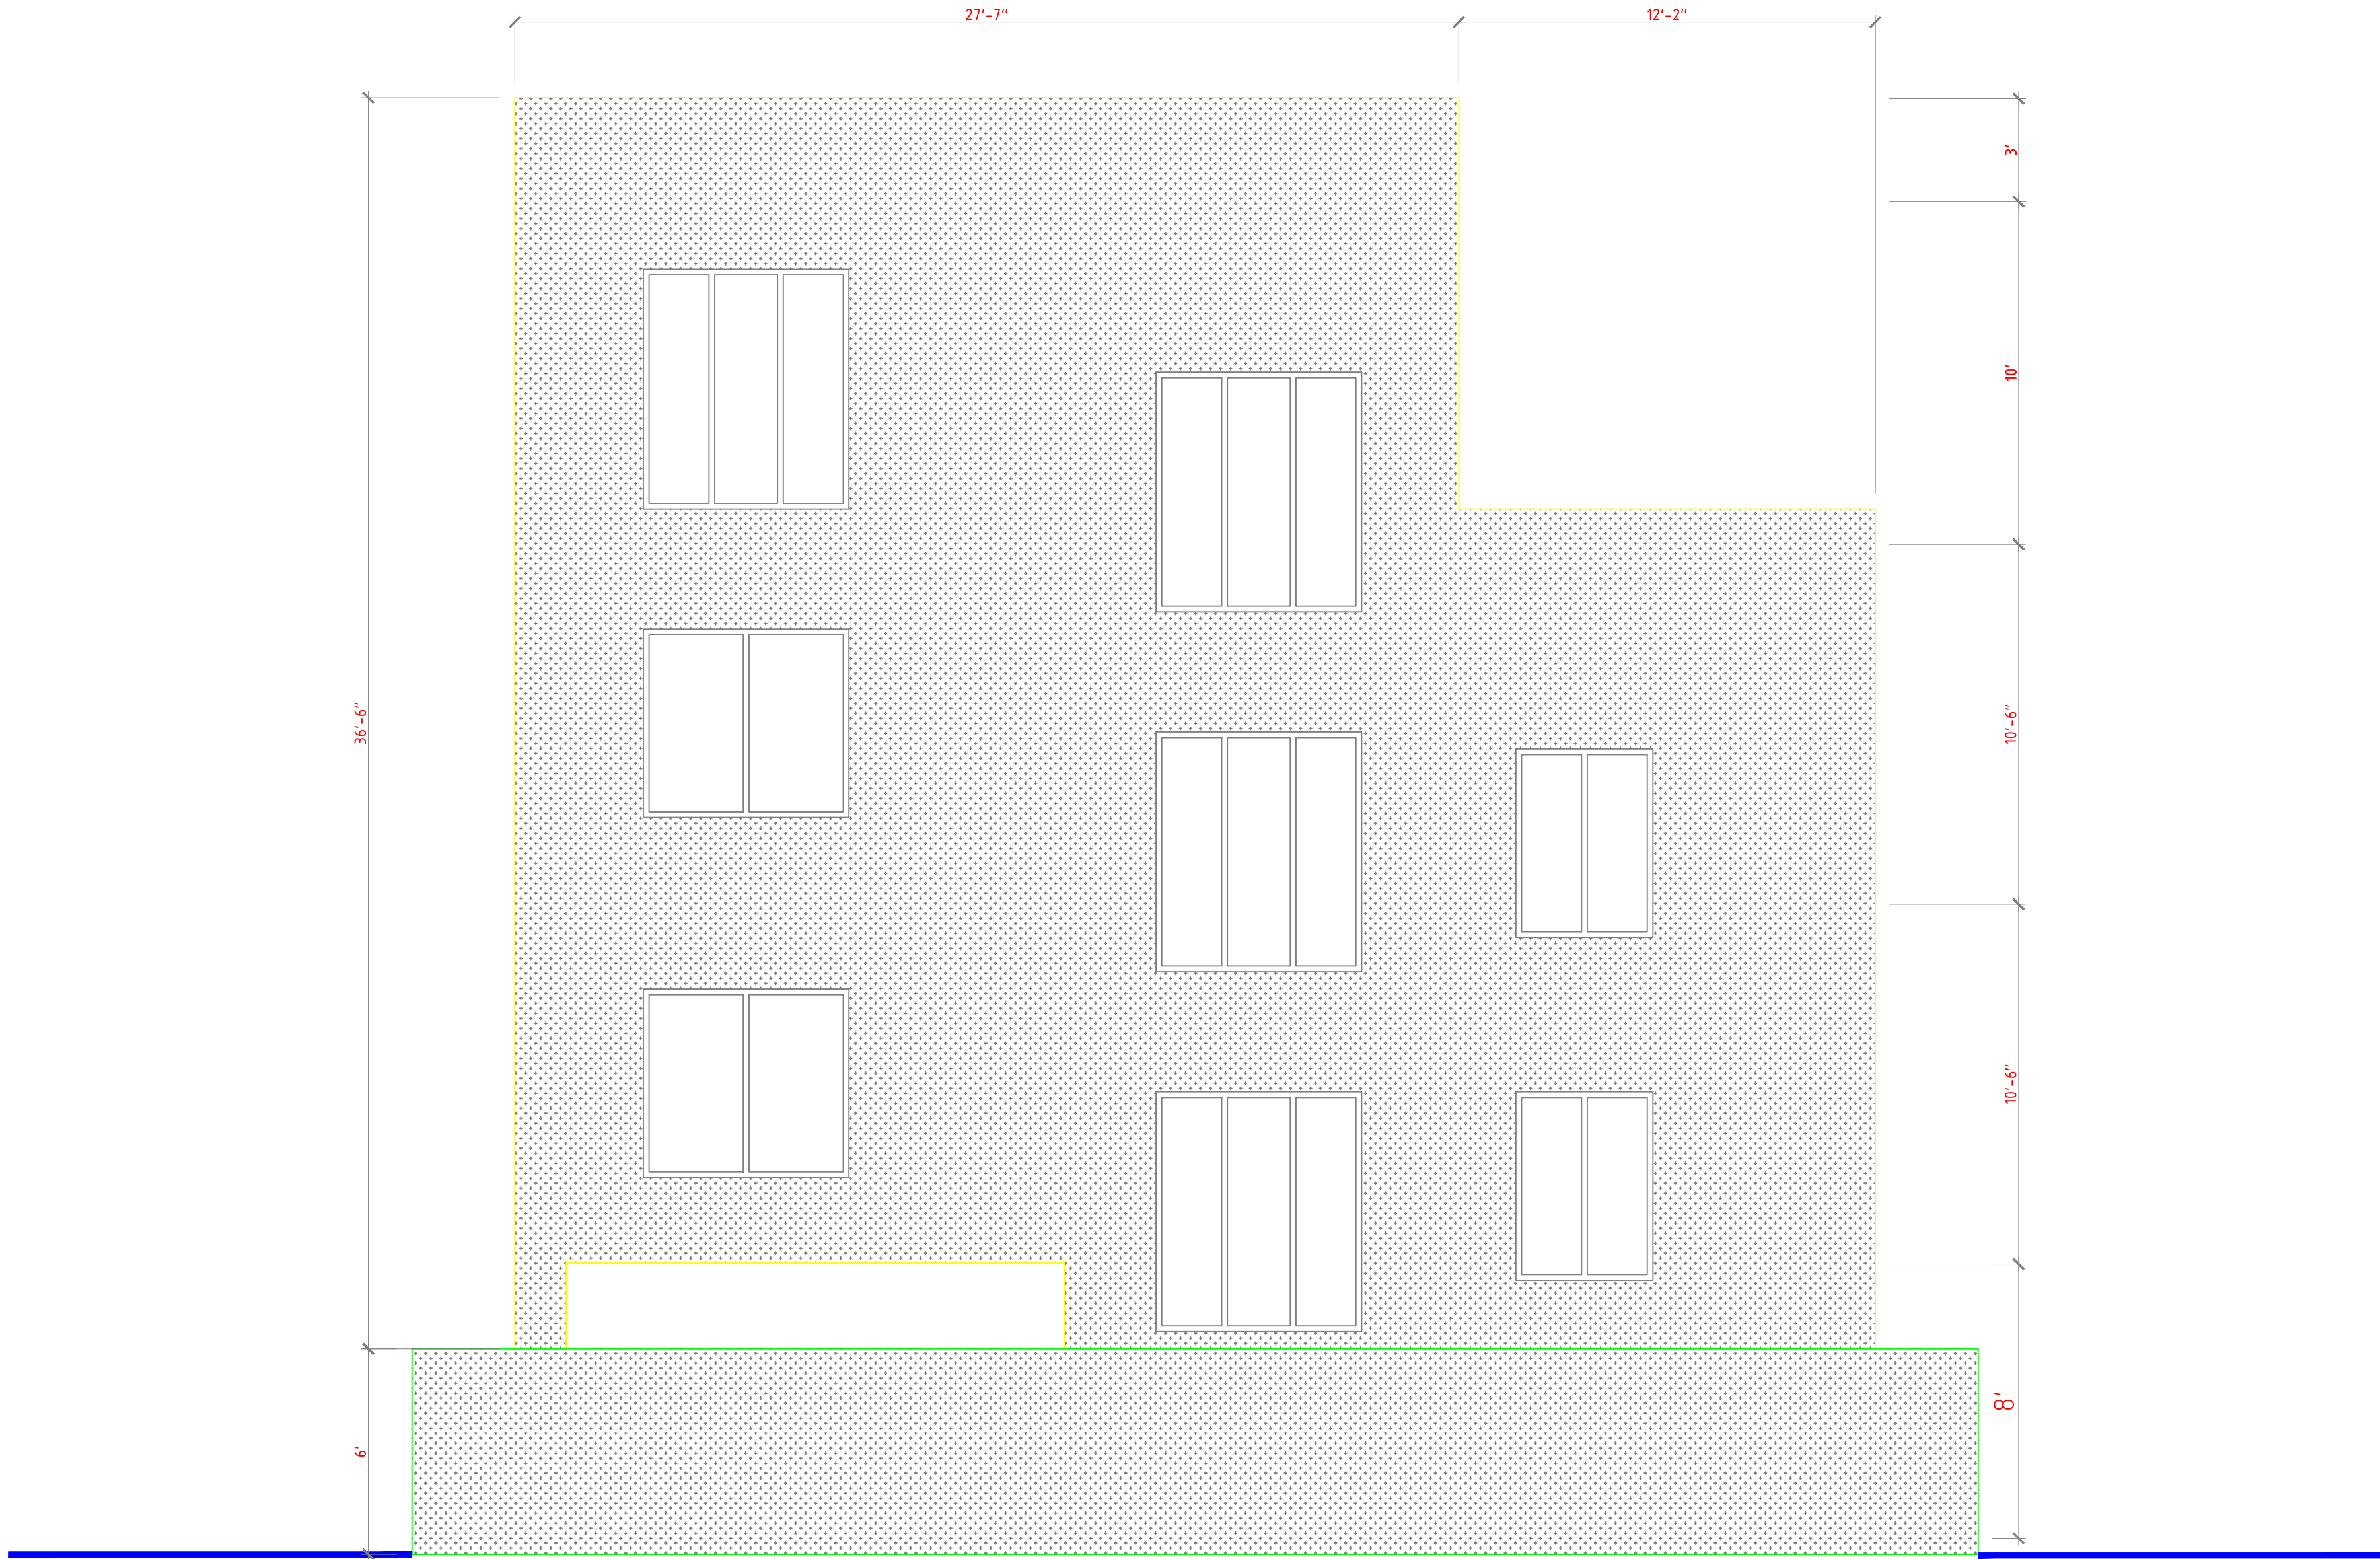
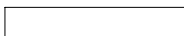


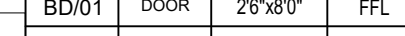

PROJECTS DETAILS :-		CLIENT DETAILS :-		AREA STATEMENT :-		PROJECT TITLE :-		DATE OF SUBMISSION :-		NORTH :-		FROM THE LEGAL TEAM		PARTNER ARCHITECTS :-		OPENING SCHEDULE					Design By :-																
Proposed Residential Villa G+2.		Mr. Narayan				SOUTH SIDE ELEVATION		07/06/2026				THE ABOVE DRAWING IS THE SOLE PROPERTY OF THE ARCHITECTS AND SHOULD NOT BE PUBLISHED OR USED OTHER WISE WITHOUT THE PRIOR CONSENT OF THE ARCHITECTS.		DSIGN CREW LLP		DT/01 DOOR 3'6"x8'0" FFL 7'0" 1 NOS		 AR.VIVEKANANDAN D.arch		 VISHAL ARCHITECTS Architects and Interiors																	
		SITE ADDRESS :-																																			
		Prestige Great Acres																																			
		REVISION NUMBER :-						SCALE :-		POWERED THROUGH :-														DT/02 DOOR 3'0"x8'0" FFL 7'0" 7 NOS		DT/03 DOOR 2'6"x8'0" FFL 7'0" 6 NOS		BD/01 DOOR 2'6"x8'0" FFL 7'0" 2 NOS		WA-01 WINDOW 8'0"x7'0" 1'0" 7'0" 2 NOS		WA-02 WINDOW 6'0"x5'6" 2'6" 7'0" 7 NOS		WA-03 WINDOW 4'0"x5'6" 2'6" 7'0" 8 NOS		VA-01 VENTILATOR 2'0"x2'0" 6'0" 7'0" 7 NOS	
		R No. R2						1:100																													