




DOOR DETAILS

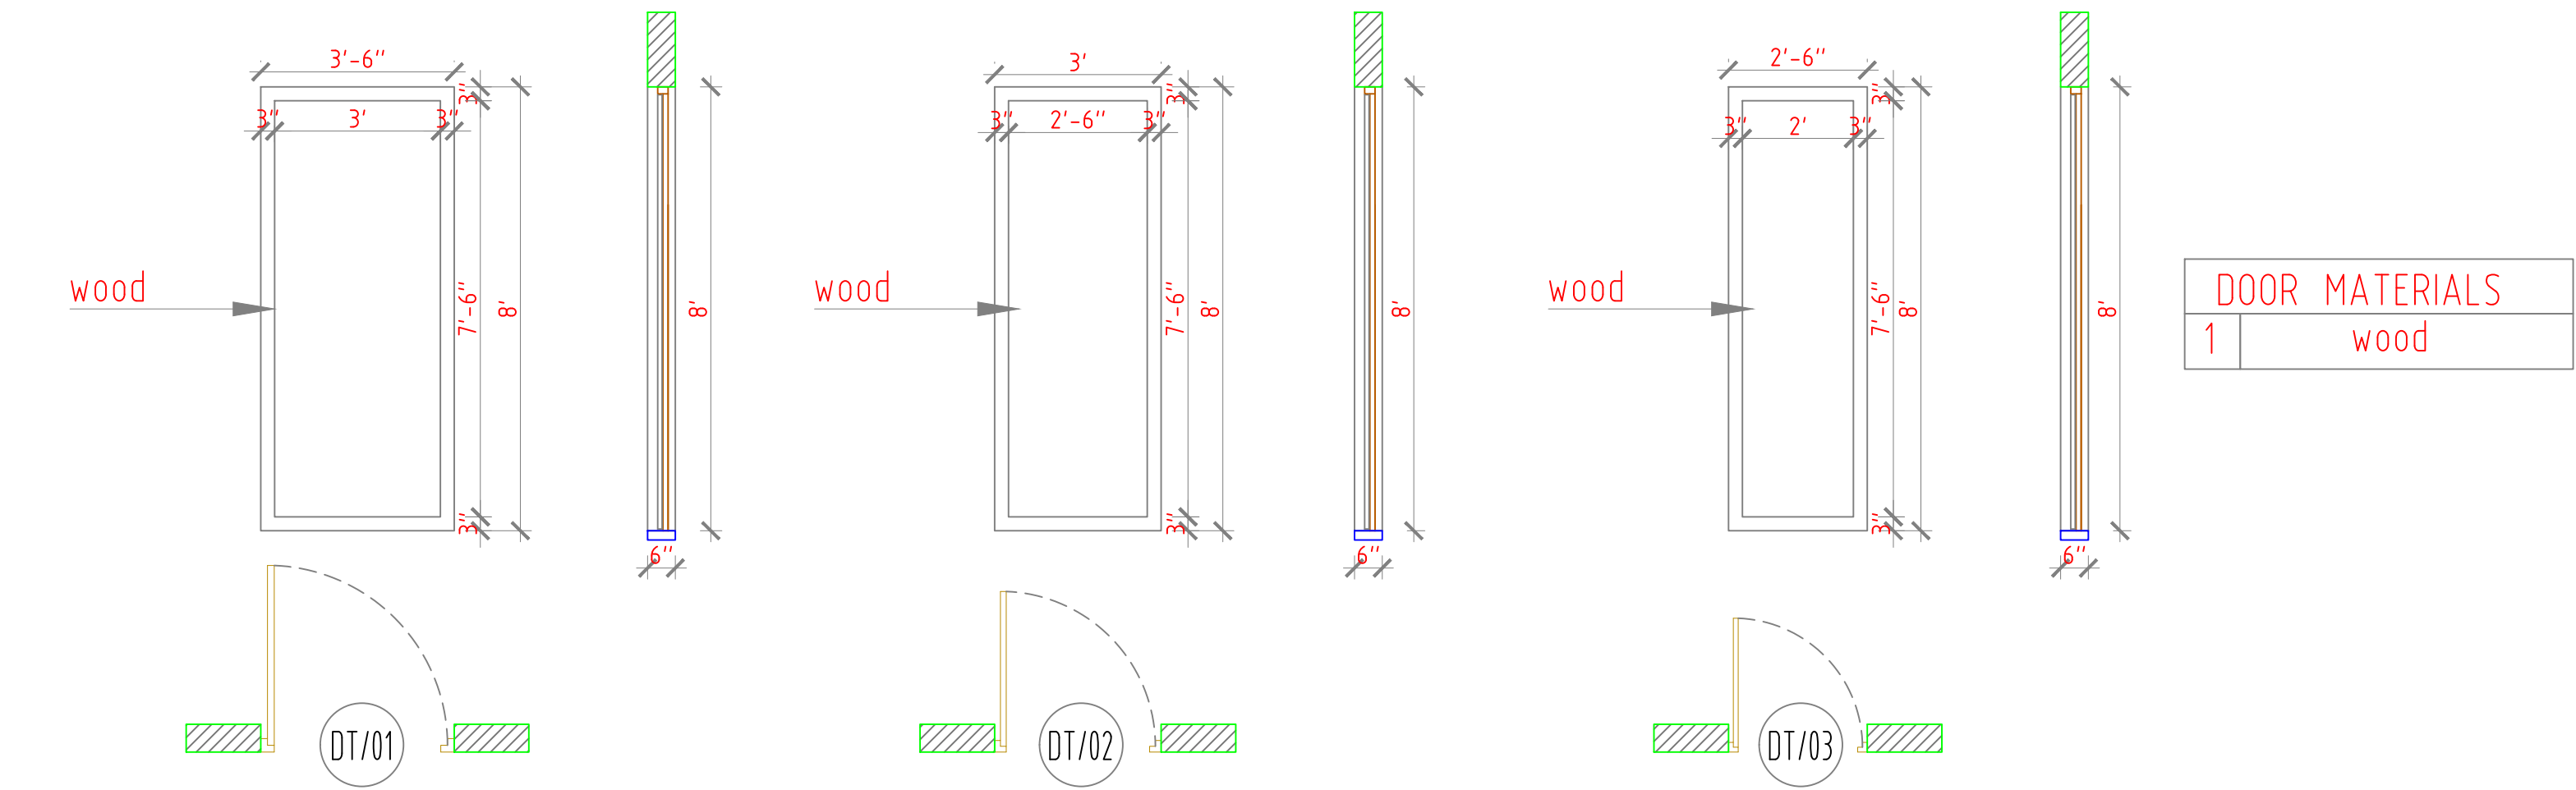


WINDOW DETAILS

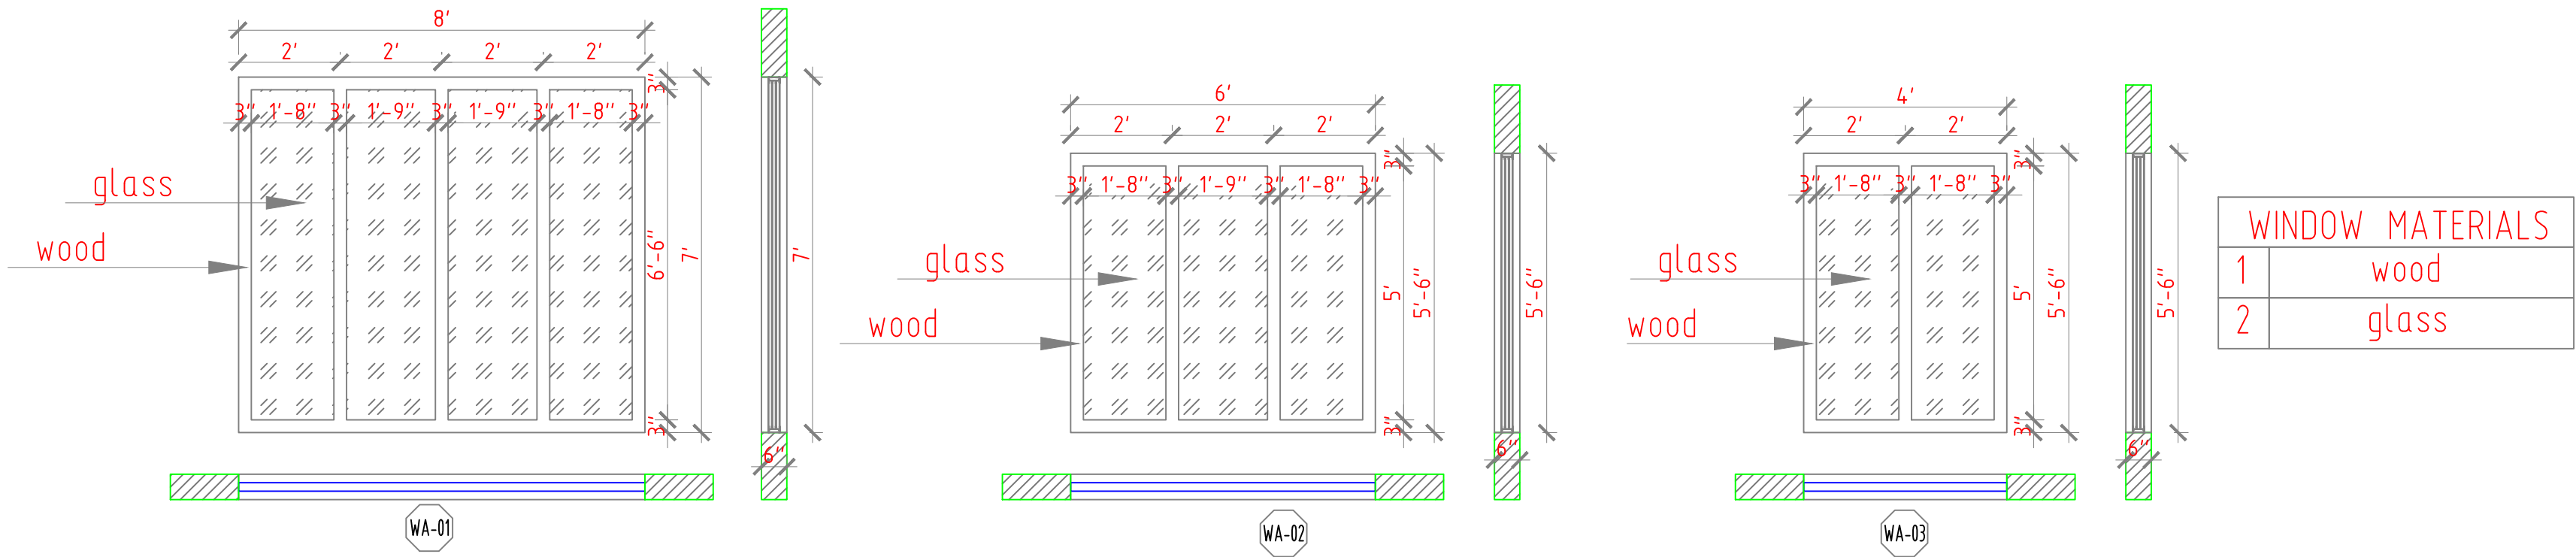

VENTILATOR DETAILS

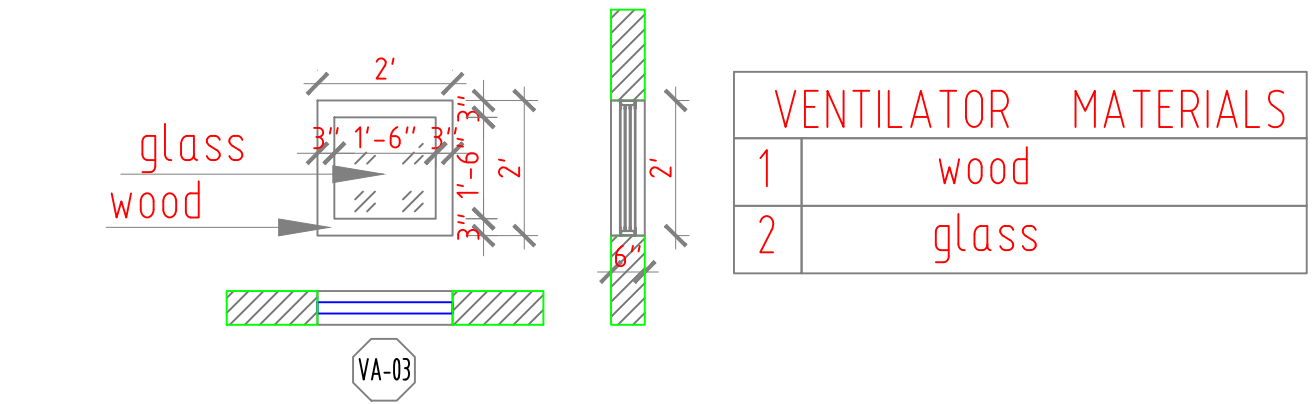

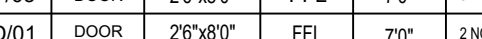PROJECTS DETAILS :-	CLIENT DETAILS :-	AREA STATEMENT :-	PROJECT TITLE :-	DATE OF SUBMISSION :-	NORTH :-	FROM THE LEGAL TEAM	PARTNER ARCHITECTS :-	OPENING SCHEDULE					Design By :-		
Proposed Residential Villa G+2.	Mr. Narayan		JOINERY DETAILS	07/06/2026		THE ABOVE DRAWING IS THE SOLE PROPERTY OF THE ARCHITECTS AND SHOULD NOT BE PUBLISHED OR USED OTHER WISE WITHOUT THE PRIOR CONSENT OF THE ARCHITECTS.	DSIGN CREW LLP			SIZE	SILL	LINTEL	NOS	 PH : 6381358459 E-mail- vishalarchitects307@gmail.com	
	SITE ADDRESS :-						DT/01	DOOR	3'6"x8'0"	FFL	7'0"	1 NOS			
	Prestige Great Acres						DT/02	DOOR	3'0"x8'0"	FFL	7'0"	7 NOS			
							DT/03	DOOR	2'6"x8'0"	FFL	7'0"	6 NOS			
				REVISION NUMBER :-	SCALE :-		POWERED THROUGH :-			BD/01	DOOR	2'6"x8'0"	FFL	7'0"	2 NOS
				R No. R2	1:100					WA-01	WINDOW	8'0"x7'0"	1'0"	7'0"	2 NOS
									WA-02	WINDOW	6'0"x5'6"	2'6"	7'0"	7 NOS	
									WA-03	WINDOW	4'0"x5'6"	2'6"	7'0"	8 NOS	
									VA-01	VENTILATOR	2'0"x2'0"	6'0"	7'0"	7 NOS	