


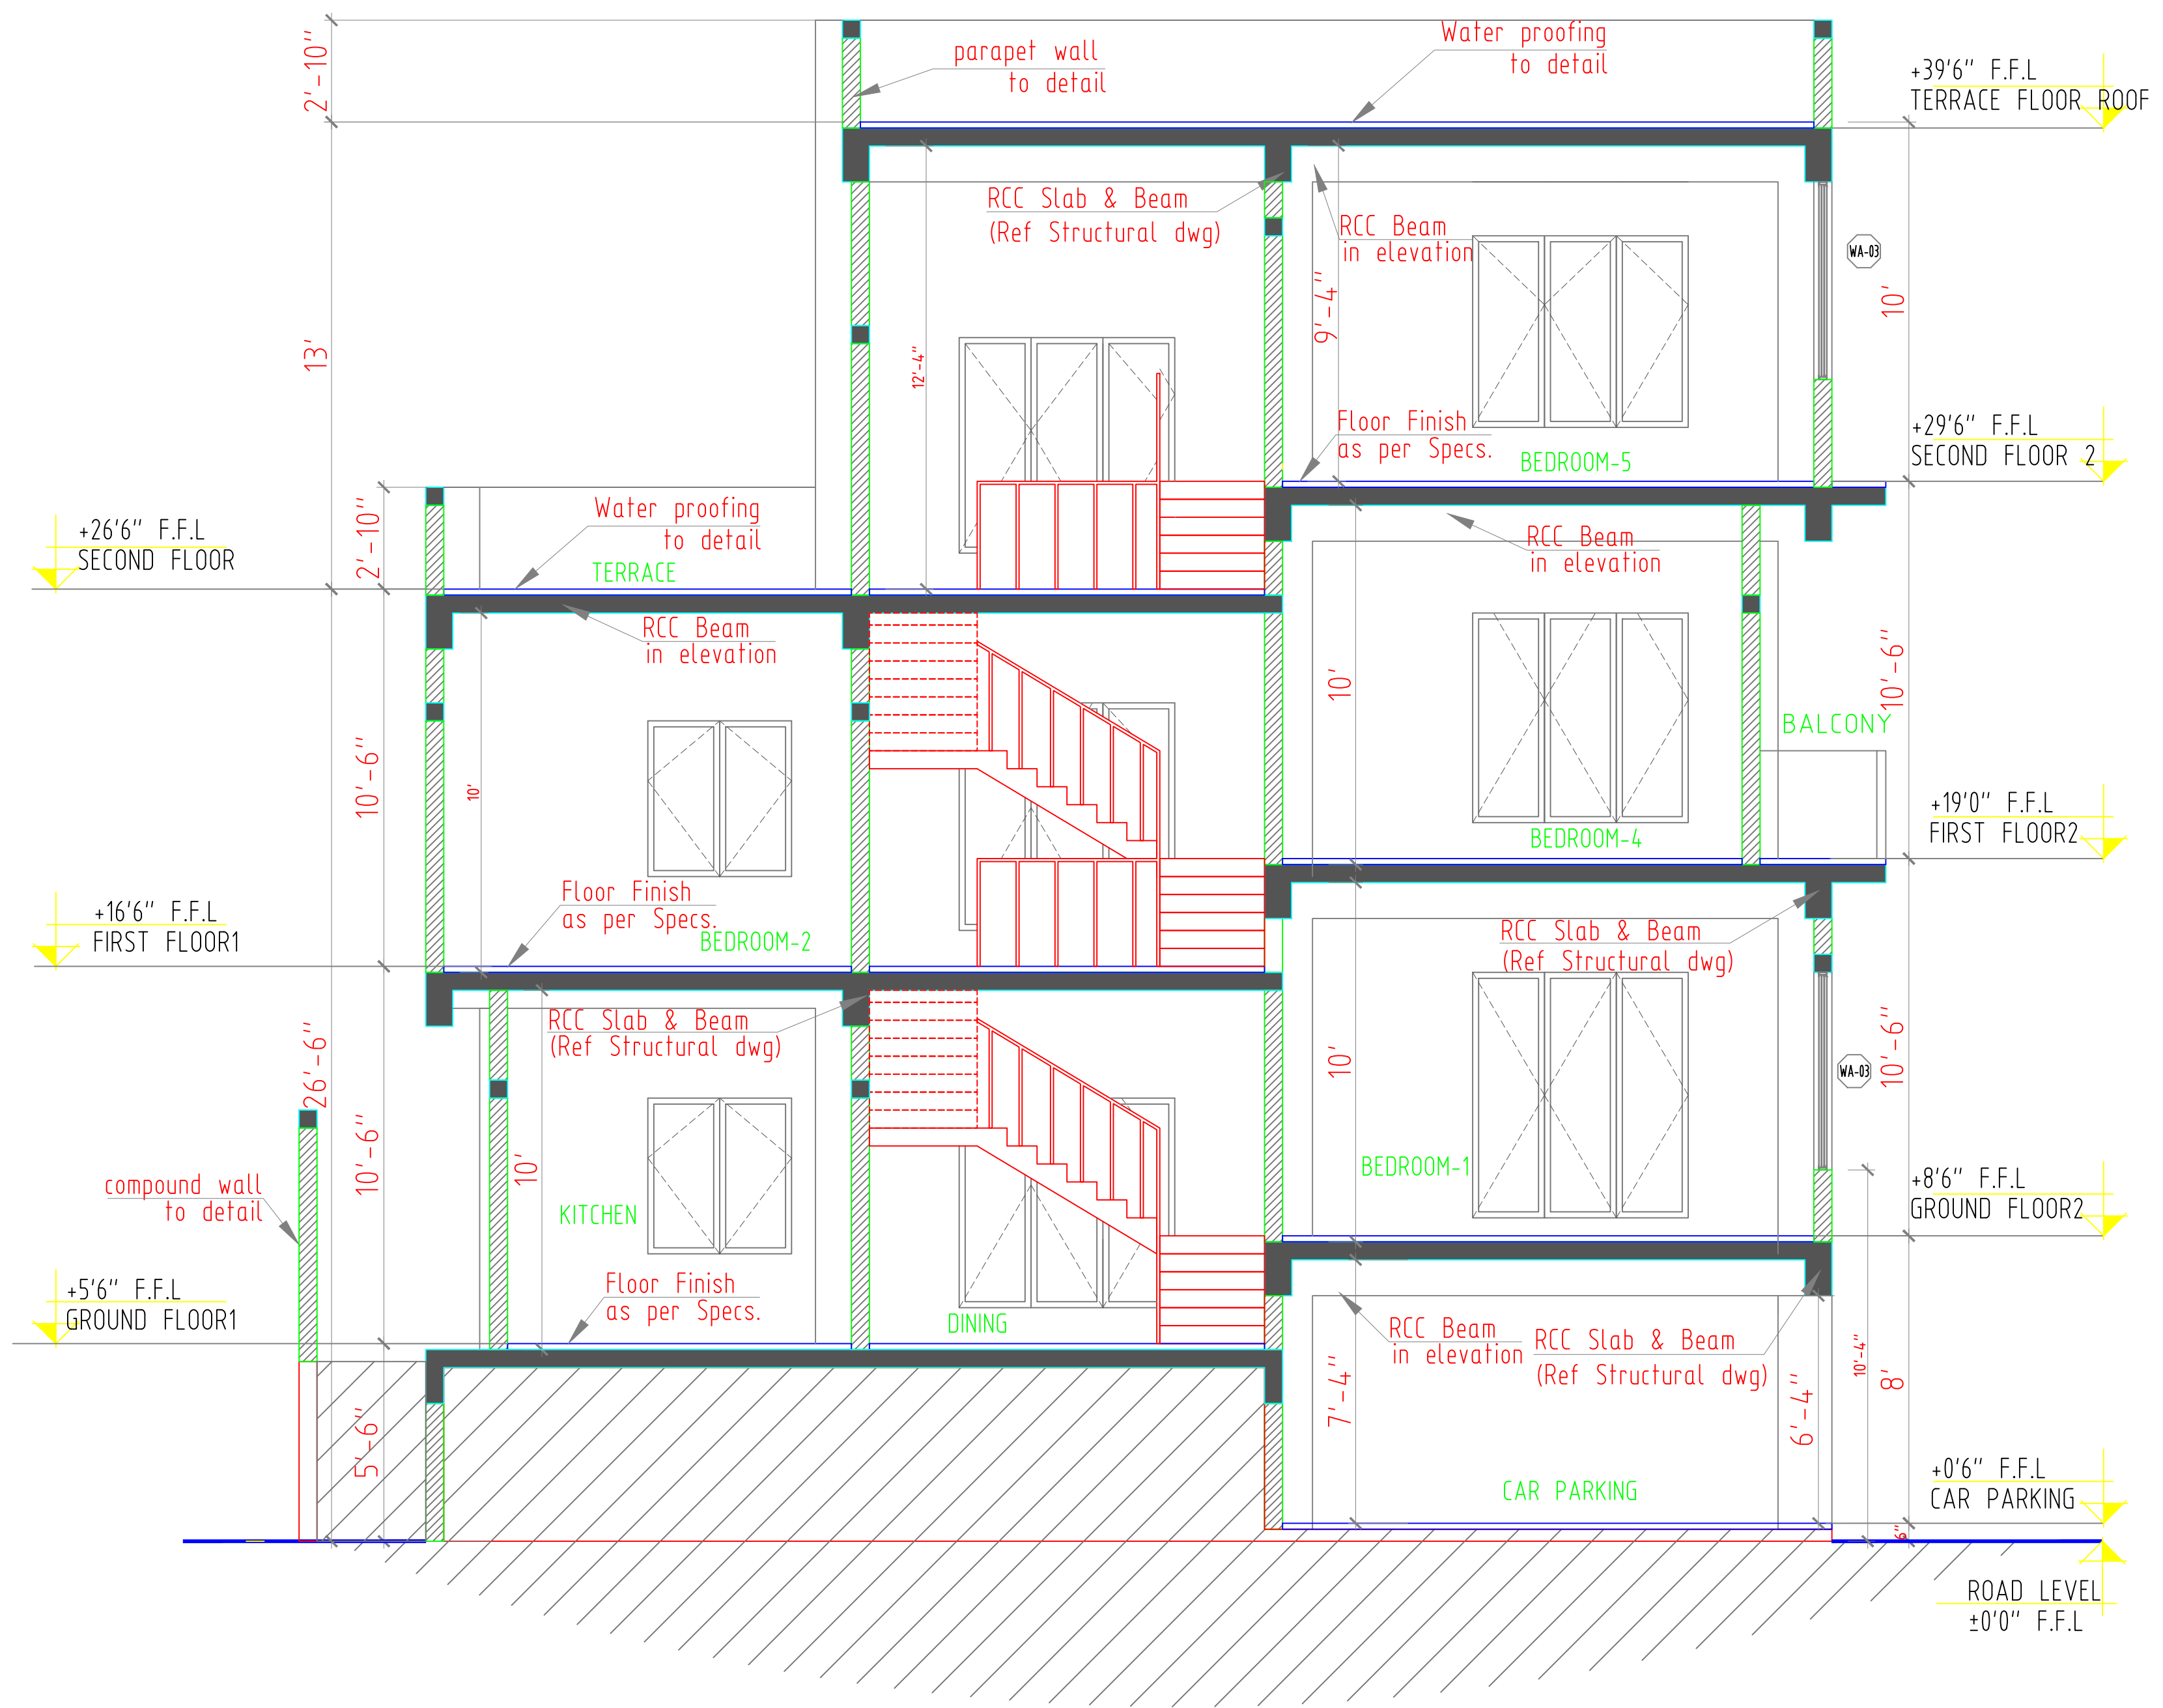

PROJECTS DETAILS :-		CLIENT DETAILS :-		AREA STATEMENT :-		PROJECT TITLE :-		DATE OF SUBMISSION :-		NORTH :-		FROM THE LEGAL TEAM		PARTNER ARCHITECTS :-		Design By :-	
Proposed Residential Villa G+2.		Mr. Narayan				SECTION - A		07/06/2026				THE ABOVE DRAWING IS THE SOLE PROPERTY OF THE ARCHITECTS AND SHOULD NOT BE PUBLISHED OR USED OTHER WISE WITHOUT THE PRIOR CONSENT OF THE ARCHITECTS		DSIGN CREW LLP		 AR.VIVEKANANDAN D.arch™ VISHAL ARCHITECTS Architects and Interiors PH : 6381358459 E-mail- vishalarchitects307@gmail.com	
		SITE ADDRESS :-						REVISION NUMBER :-		SCALE :-	
		Prestige Great Acres						R No. R2		1:100	
																POWERED THROUGH :- 	
																<table><thead><tr><th colspan="6">OPENING SCHEDULE</th></tr><tr><th></th><th></th><th>SIZE</th><th>SILL</th><th>LINTEL</th><th>NOS</th></tr></thead><tbody><tr><td>DT/01</td><td>DOOR</td><td>3'6"x8'0"</td><td>FFL</td><td>7'0"</td><td>1 NOS</td></tr><tr><td>DT/02</td><td>DOOR</td><td>3'0"x8'0"</td><td>FFL</td><td>7'0"</td><td>7 NOS</td></tr><tr><td>DT/03</td><td>DOOR</td><td>2'6"x8'0"</td><td>FFL</td><td>7'0"</td><td>6 NOS</td></tr><tr><td>BD/01</td><td>DOOR</td><td>2'6"x8'0"</td><td>FFL</td><td>7'0"</td><td>2 NOS</td></tr><tr><td>WA-01</td><td>WINDOW</td><td>8'0"x7'0"</td><td>10"</td><td>7'0"</td><td>2 NOS</td></tr><tr><td>WA-02</td><td>WINDOW</td><td>6'0"x5'6"</td><td>2'6"</td><td>7'0"</td><td>7 NOS</td></tr><tr><td>WA-03</td><td>WINDOW</td><td>4'0"x5'6"</td><td>2'6"</td><td>7'0"</td><td>8 NOS</td></tr><tr><td>VA-01</td><td>VENTILATOR</td><td>2'0"x2'0"</td><td>6'0"</td><td>7'0"</td><td>7 NOS</td></tr></tbody></table>						OPENING SCHEDULE								SIZE	SILL	LINTEL	NOS	DT/01	DOOR	3'6"x8'0"	FFL	7'0"	1 NOS	DT/02	DOOR	3'0"x8'0"	FFL	7'0"	7 NOS	DT/03	DOOR	2'6"x8'0"	FFL	7'0"	6 NOS	BD/01	DOOR	2'6"x8'0"	FFL	7'0"	2 NOS	WA-01	WINDOW	8'0"x7'0"	10"	7'0"	2 NOS	WA-02	WINDOW	6'0"x5'6"	2'6"	7'0"	7 NOS	WA-03	WINDOW	4'0"x5'6"	2'6"	7'0"	8 NOS	VA-01	VENTILATOR	2'0"x2'0"	6'0"	7'0"	7 NOS
OPENING SCHEDULE	
		SIZE	SILL	LINTEL	NOS	
DT/01	DOOR	3'6"x8'0"	FFL	7'0"	1 NOS	
DT/02	DOOR	3'0"x8'0"	FFL	7'0"	7 NOS	
DT/03	DOOR	2'6"x8'0"	FFL	7'0"	6 NOS	
BD/01	DOOR	2'6"x8'0"	FFL	7'0"	2 NOS	
WA-01	WINDOW	8'0"x7'0"	10"	7'0"	2 NOS	
WA-02	WINDOW	6'0"x5'6"	2'6"	7'0"	7 NOS	
WA-03	WINDOW	4'0"x5'6"	2'6"	7'0"	8 NOS	
VA-01	VENTILATOR	2'0"x2'0"	6'0"	7'0"	7 NOS	