
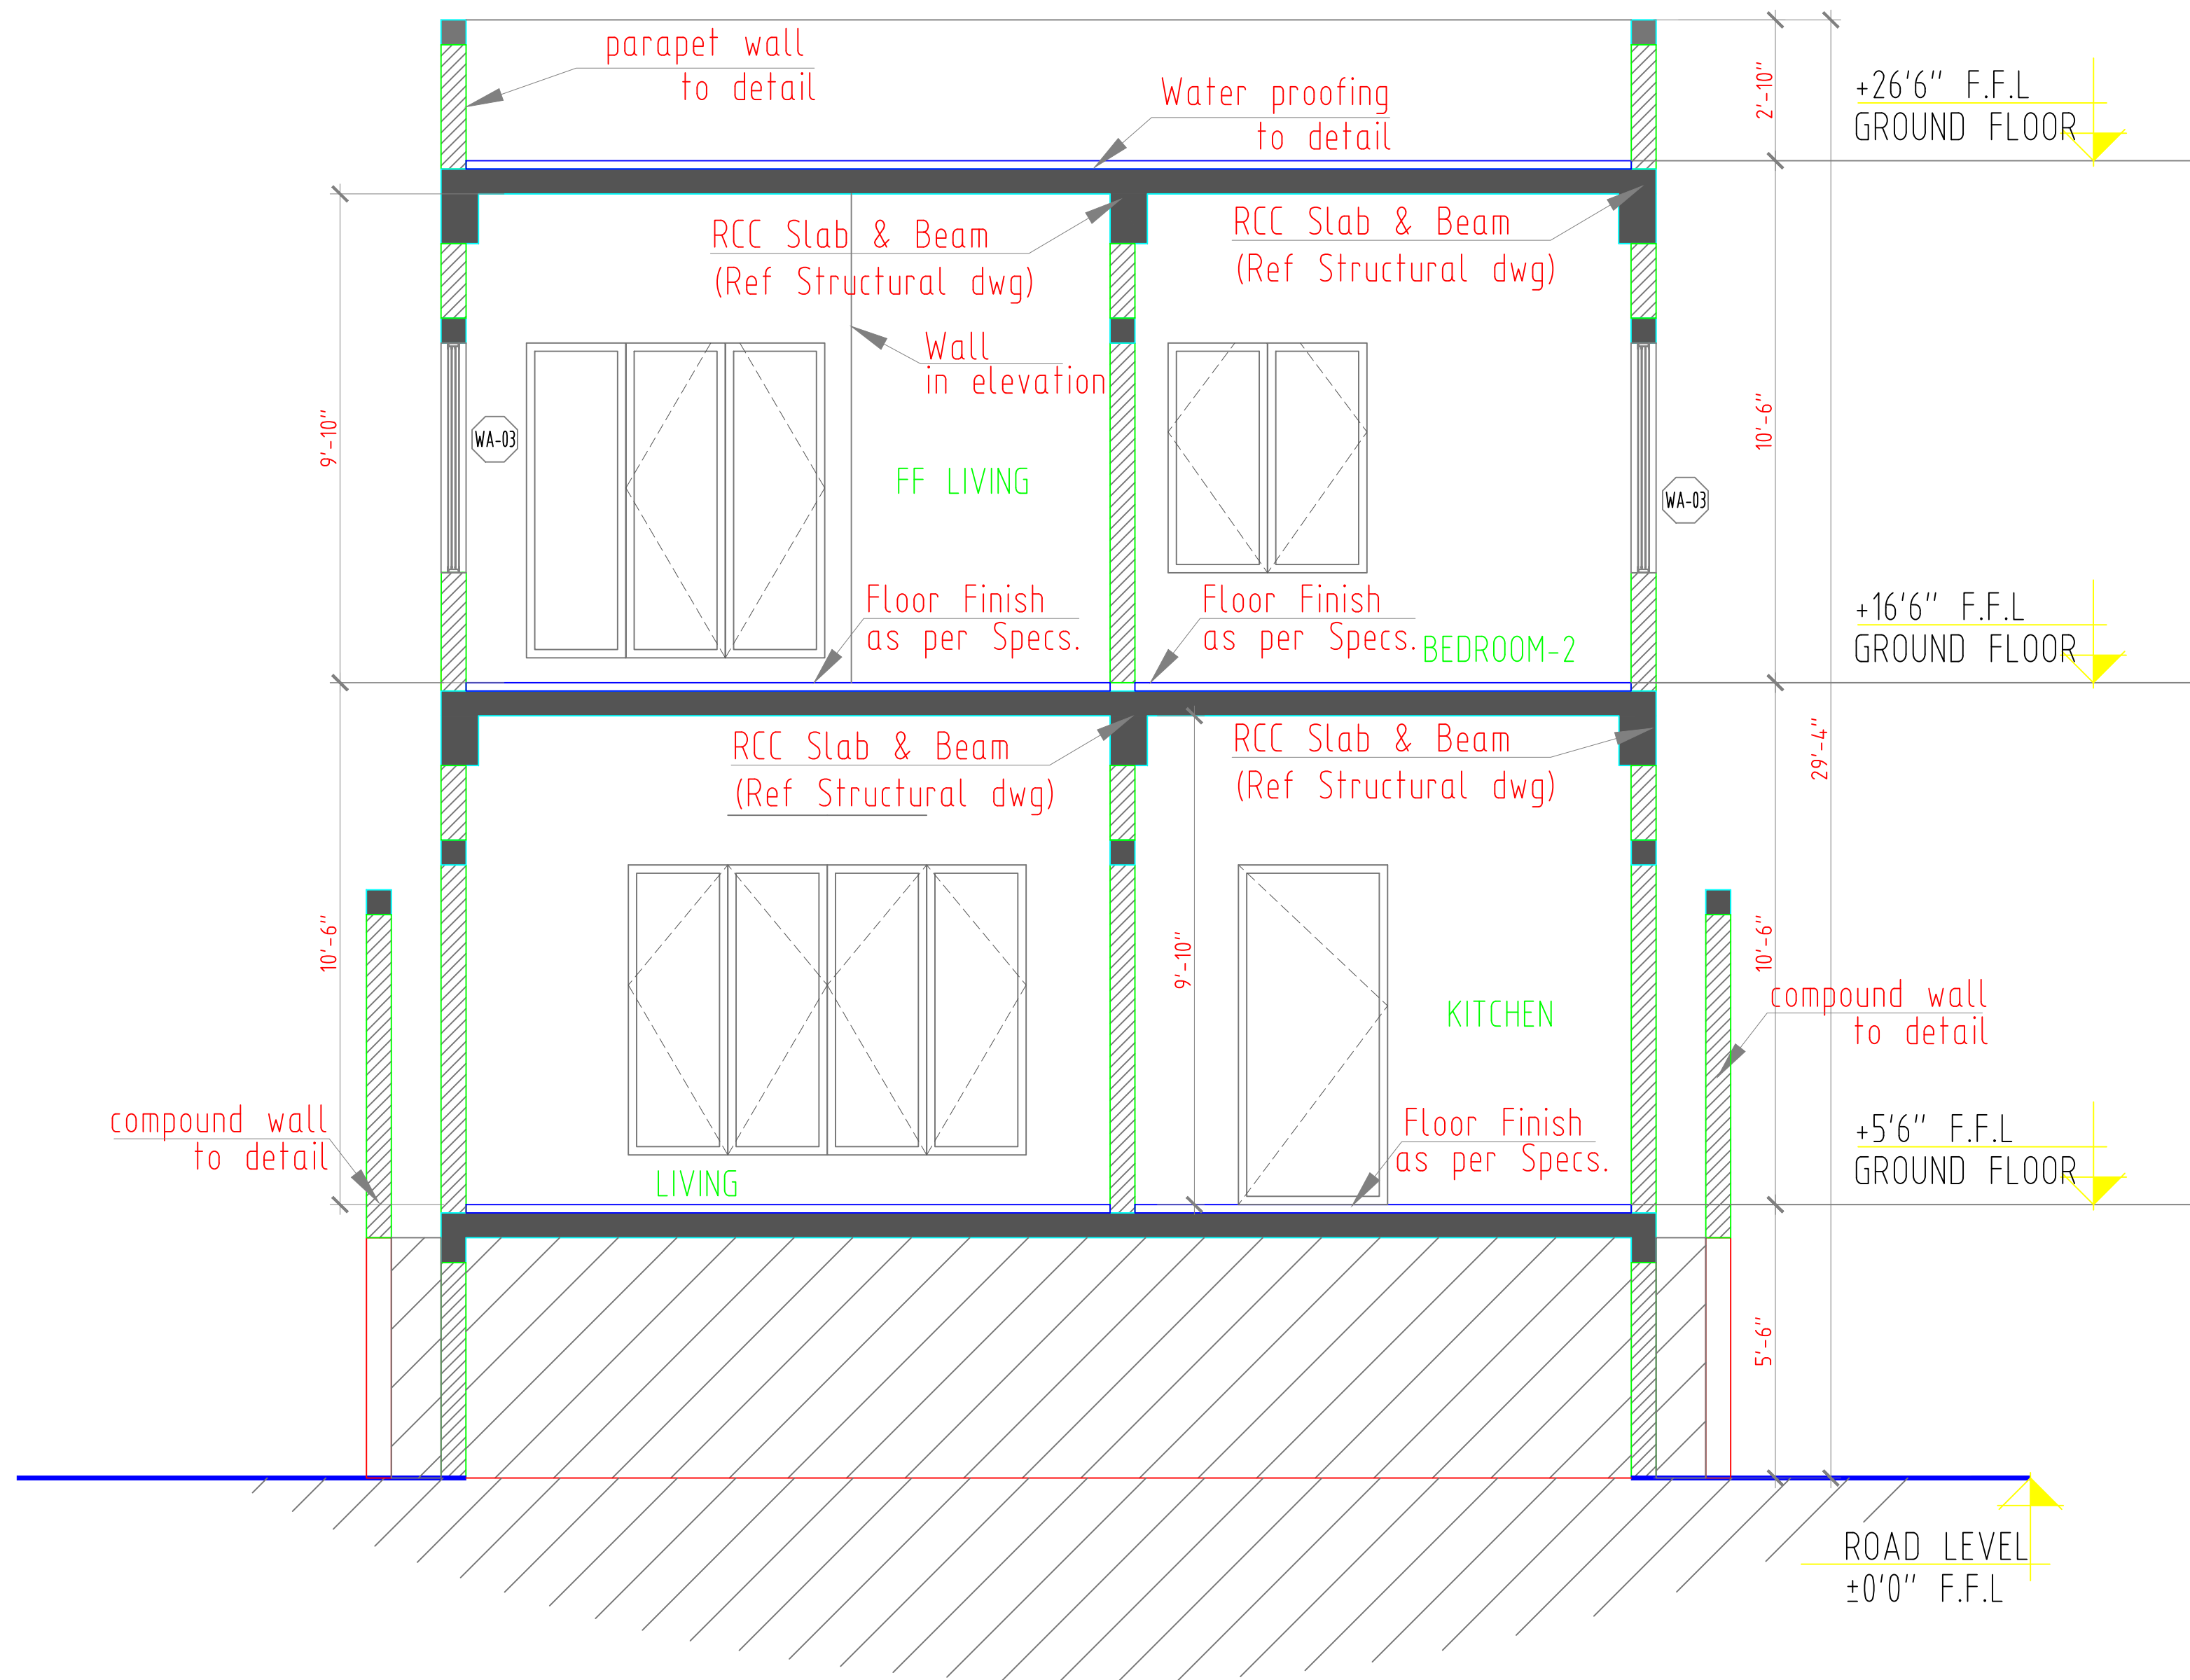


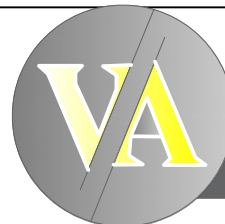

PROJECTS DETAILS :-		CLIENT DETAILS :-	AREA STATEMENT :-	PROJECT TITLE :-	DATE OF SUBMISSION :-	NORTH :-	FROM THE LEGAL TEAM	PARTNER ARCHITECTS :-	OPENING SCHEDULE					Design By :-	
Proposed Residential Villa G+2.		Mr. Narayan		SECTION - B	07/06/2026		THE ABOVE DRAWING IS THE SOLE PROPERTY OF THE ARCHITECTS AND SHOULD NOT BE PUBLISHED OR USED OTHER WISE WITHOUT THE PRIOR CONSENT OF THE ARCHITECTS.	DSIGN CREW LLP	DT/01	DOOR	3'6"x8'0"	FFL	7'0"	1 NOS	 AR.VIVEKANANDAN D.arch VISHAL ARCHITECTS Architects and Interiors PH : 6381358459 E-mail- vishalarchitects307@gmail.com
		SITE ADDRESS :-				DT/02			DOOR	3'0"x8'0"	FFL	7'0"	7 NOS		
		Prestige Great Acres				DT/03			DOOR	2'6"x8'0"	FFL	7'0"	6 NOS		
						BD/01			DOOR	2'6"x8'0"	FFL	7'0"	2 NOS		
						WA-01			WINDOW	8'0"x7'0"	1'0"	7'0"	2 NOS		
					REVISION NUMBER :-	SCALE :-		POWERED THROUGH :-	WA-02	WINDOW	6'0"x5'6"	2'6"	7'0"	7 NOS	
					R No. R2	1:100			WA-03	WINDOW	4'0"x5'6"	2'6"	7'0"	8 NOS	
									VA-01	VENTILATOR	2'0"x2'0"	6'0"	7'0"	7 NOS	