



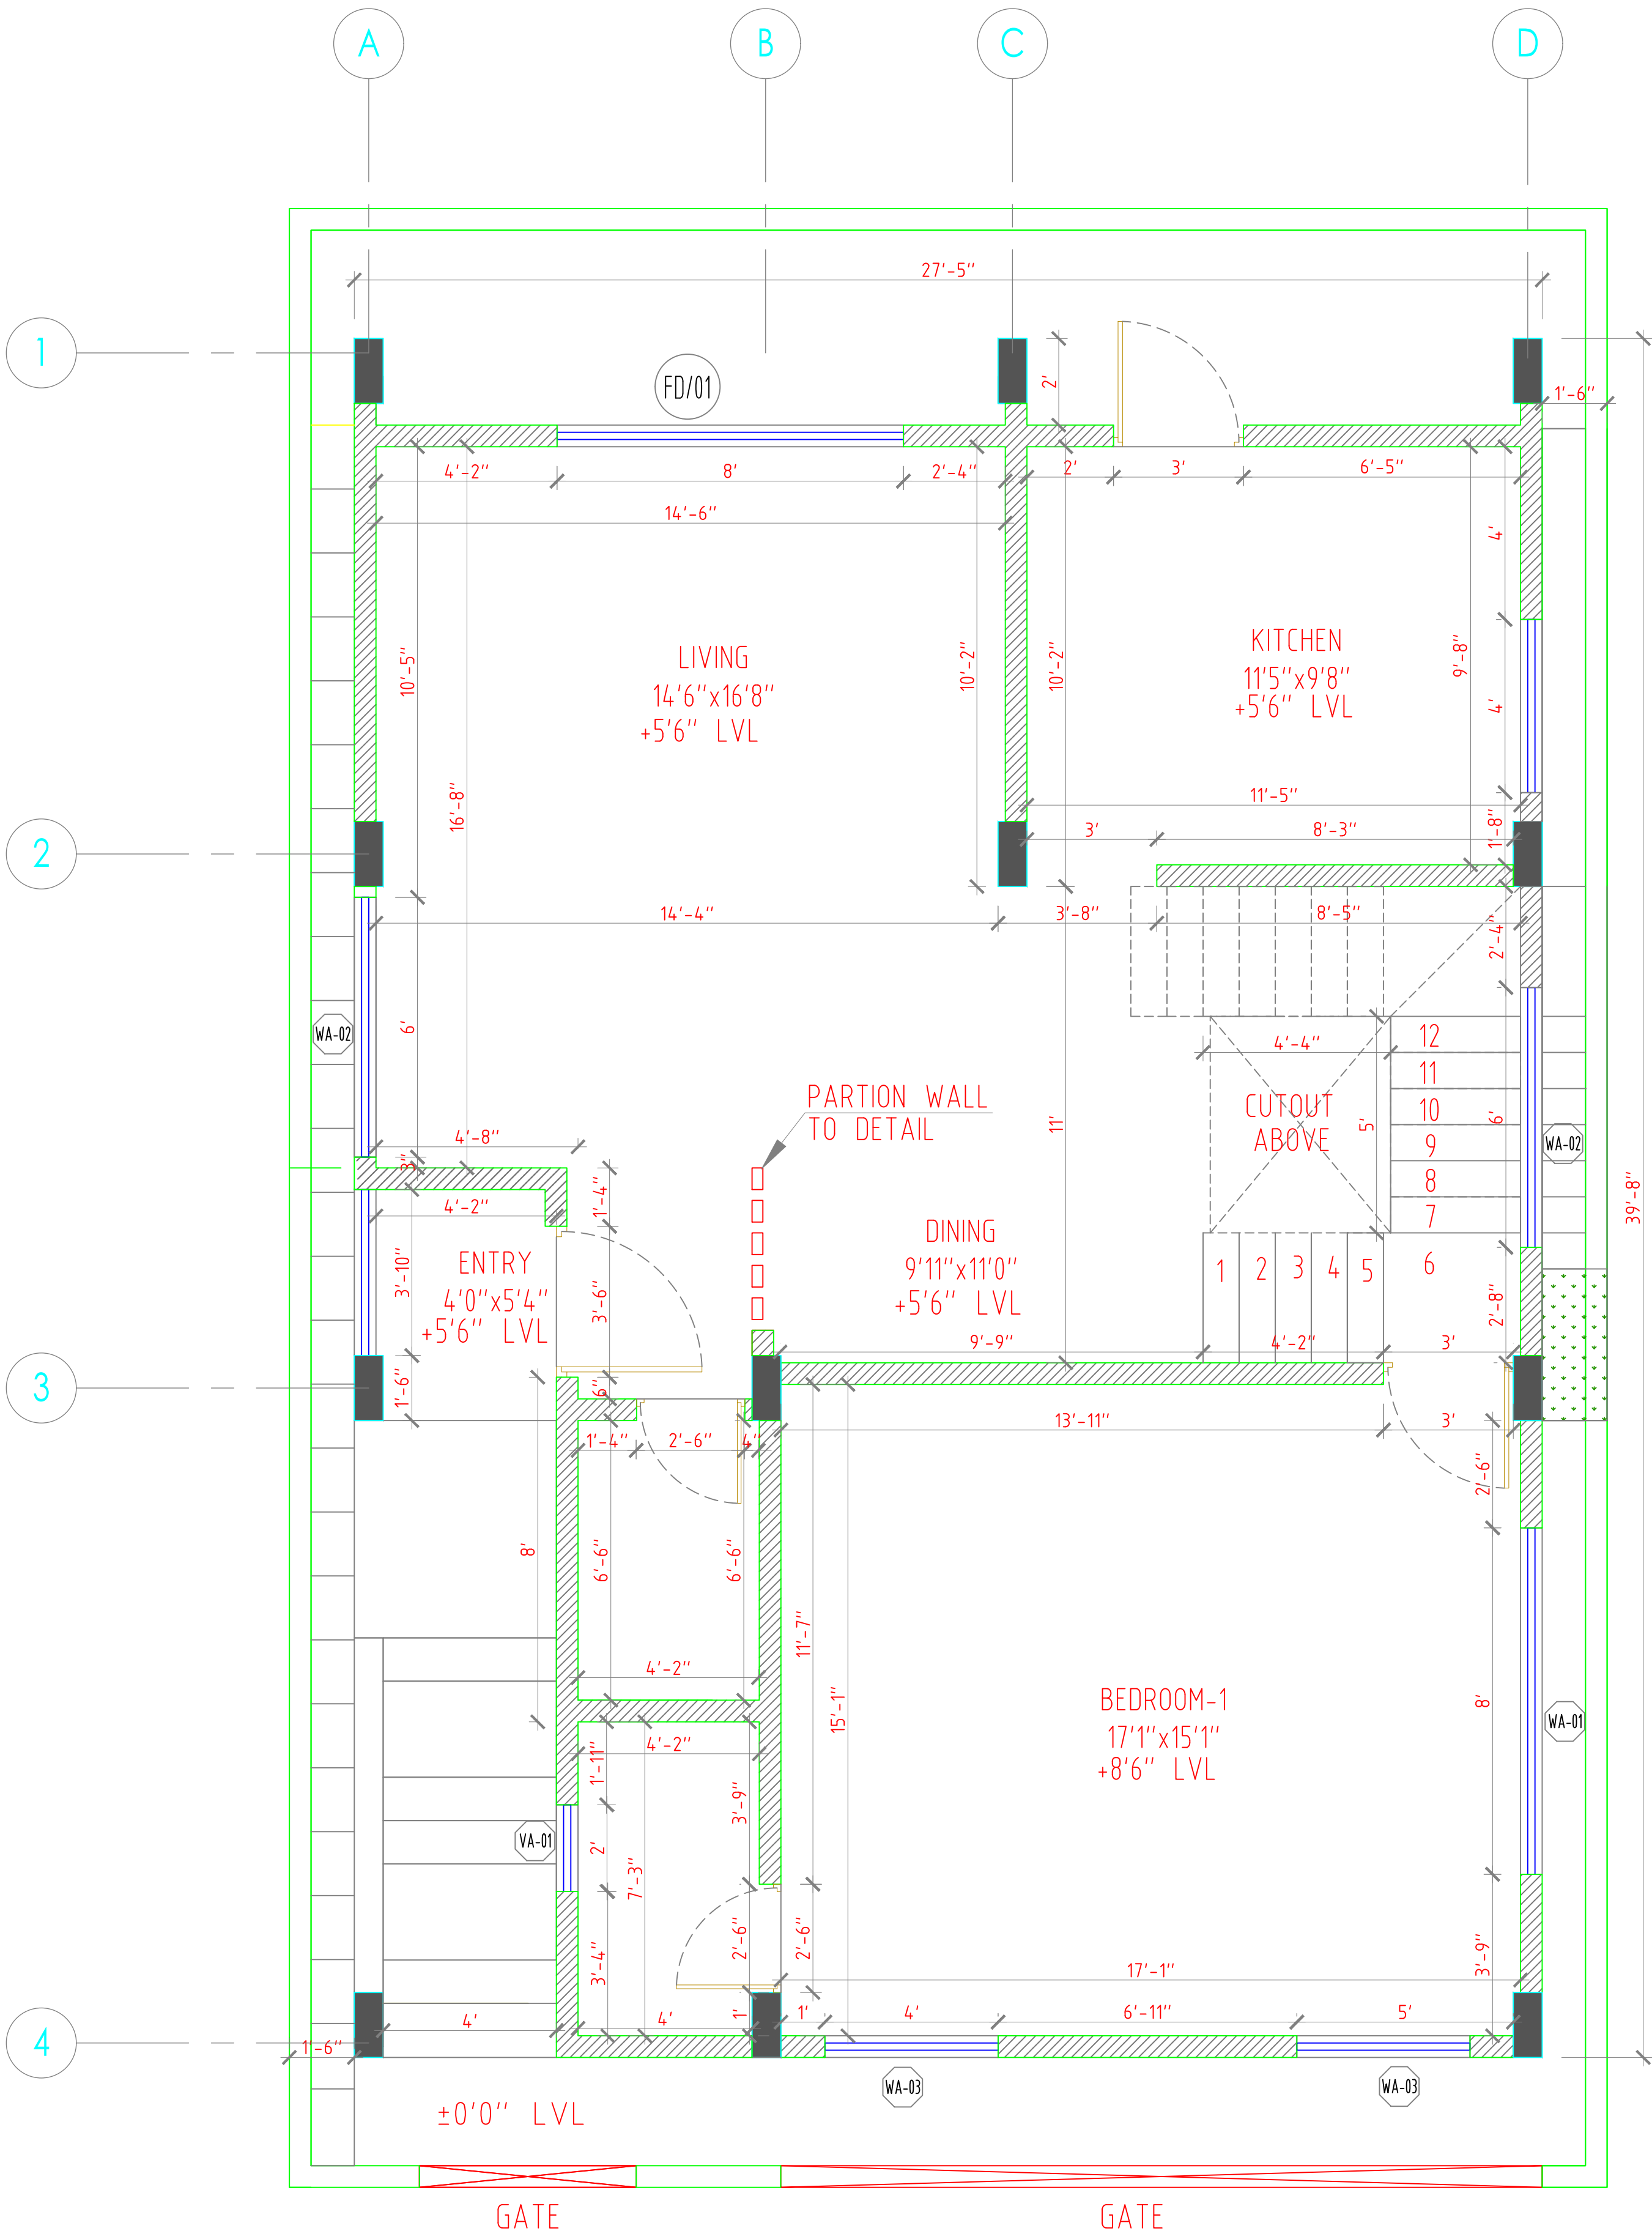

GROUND FLOOR PLAN - LEVEL 1 01

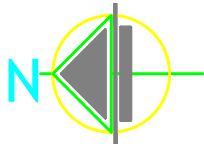

PROJECTS DETAILS :-		CLIENT DETAILS :-		AREA STATEMENT :-		PROJECT TITLE :-		DATE OF SUBMISSION :-		NORTH :-		FROM THE LEGAL TEAM		PARTNER ARCHITECTS :-		OPENING SCHEDULE		Design By :-			
Proposed Residential Villa G+2.		Mr. Narayan				Ground Floor Plan Level 1 GFC		07/06/2026				THE ABOVE DRAWING IS THE SOLE PROPERTY OF THE ARCHITECTS AND SHOULD NOT BE PUBLISHED OR USED OTHER WISE WITHOUT THE PRIOR CONSENT OF THE ARCHITECTS.		DSIGN CREW LLP		DT/01 DOOR 36"x80" FFL 7'0" 1 NOS		 AR.VIVEKANANDAN VISHAL ARCHITECTS Architects and Interiors PH : 6381358458 E-mail: vishalarchitects307@gmail.com			
		SITE ADDRESS :-						REVISION NUMBER :-		R No. R2						1:100				DT/02 DOOR 30"x80" FFL 7'0" 7 NOS	
		Prestige Great Acres																		DT/03 DOOR 26"x80" FFL 7'0" 6 NOS	
																				BD/01 DOOR 26"x80" FFL 7'0" 2 NOS	
																				WA-01 WINDOW 80"x70" 10" 7'0" 2 NOS	