

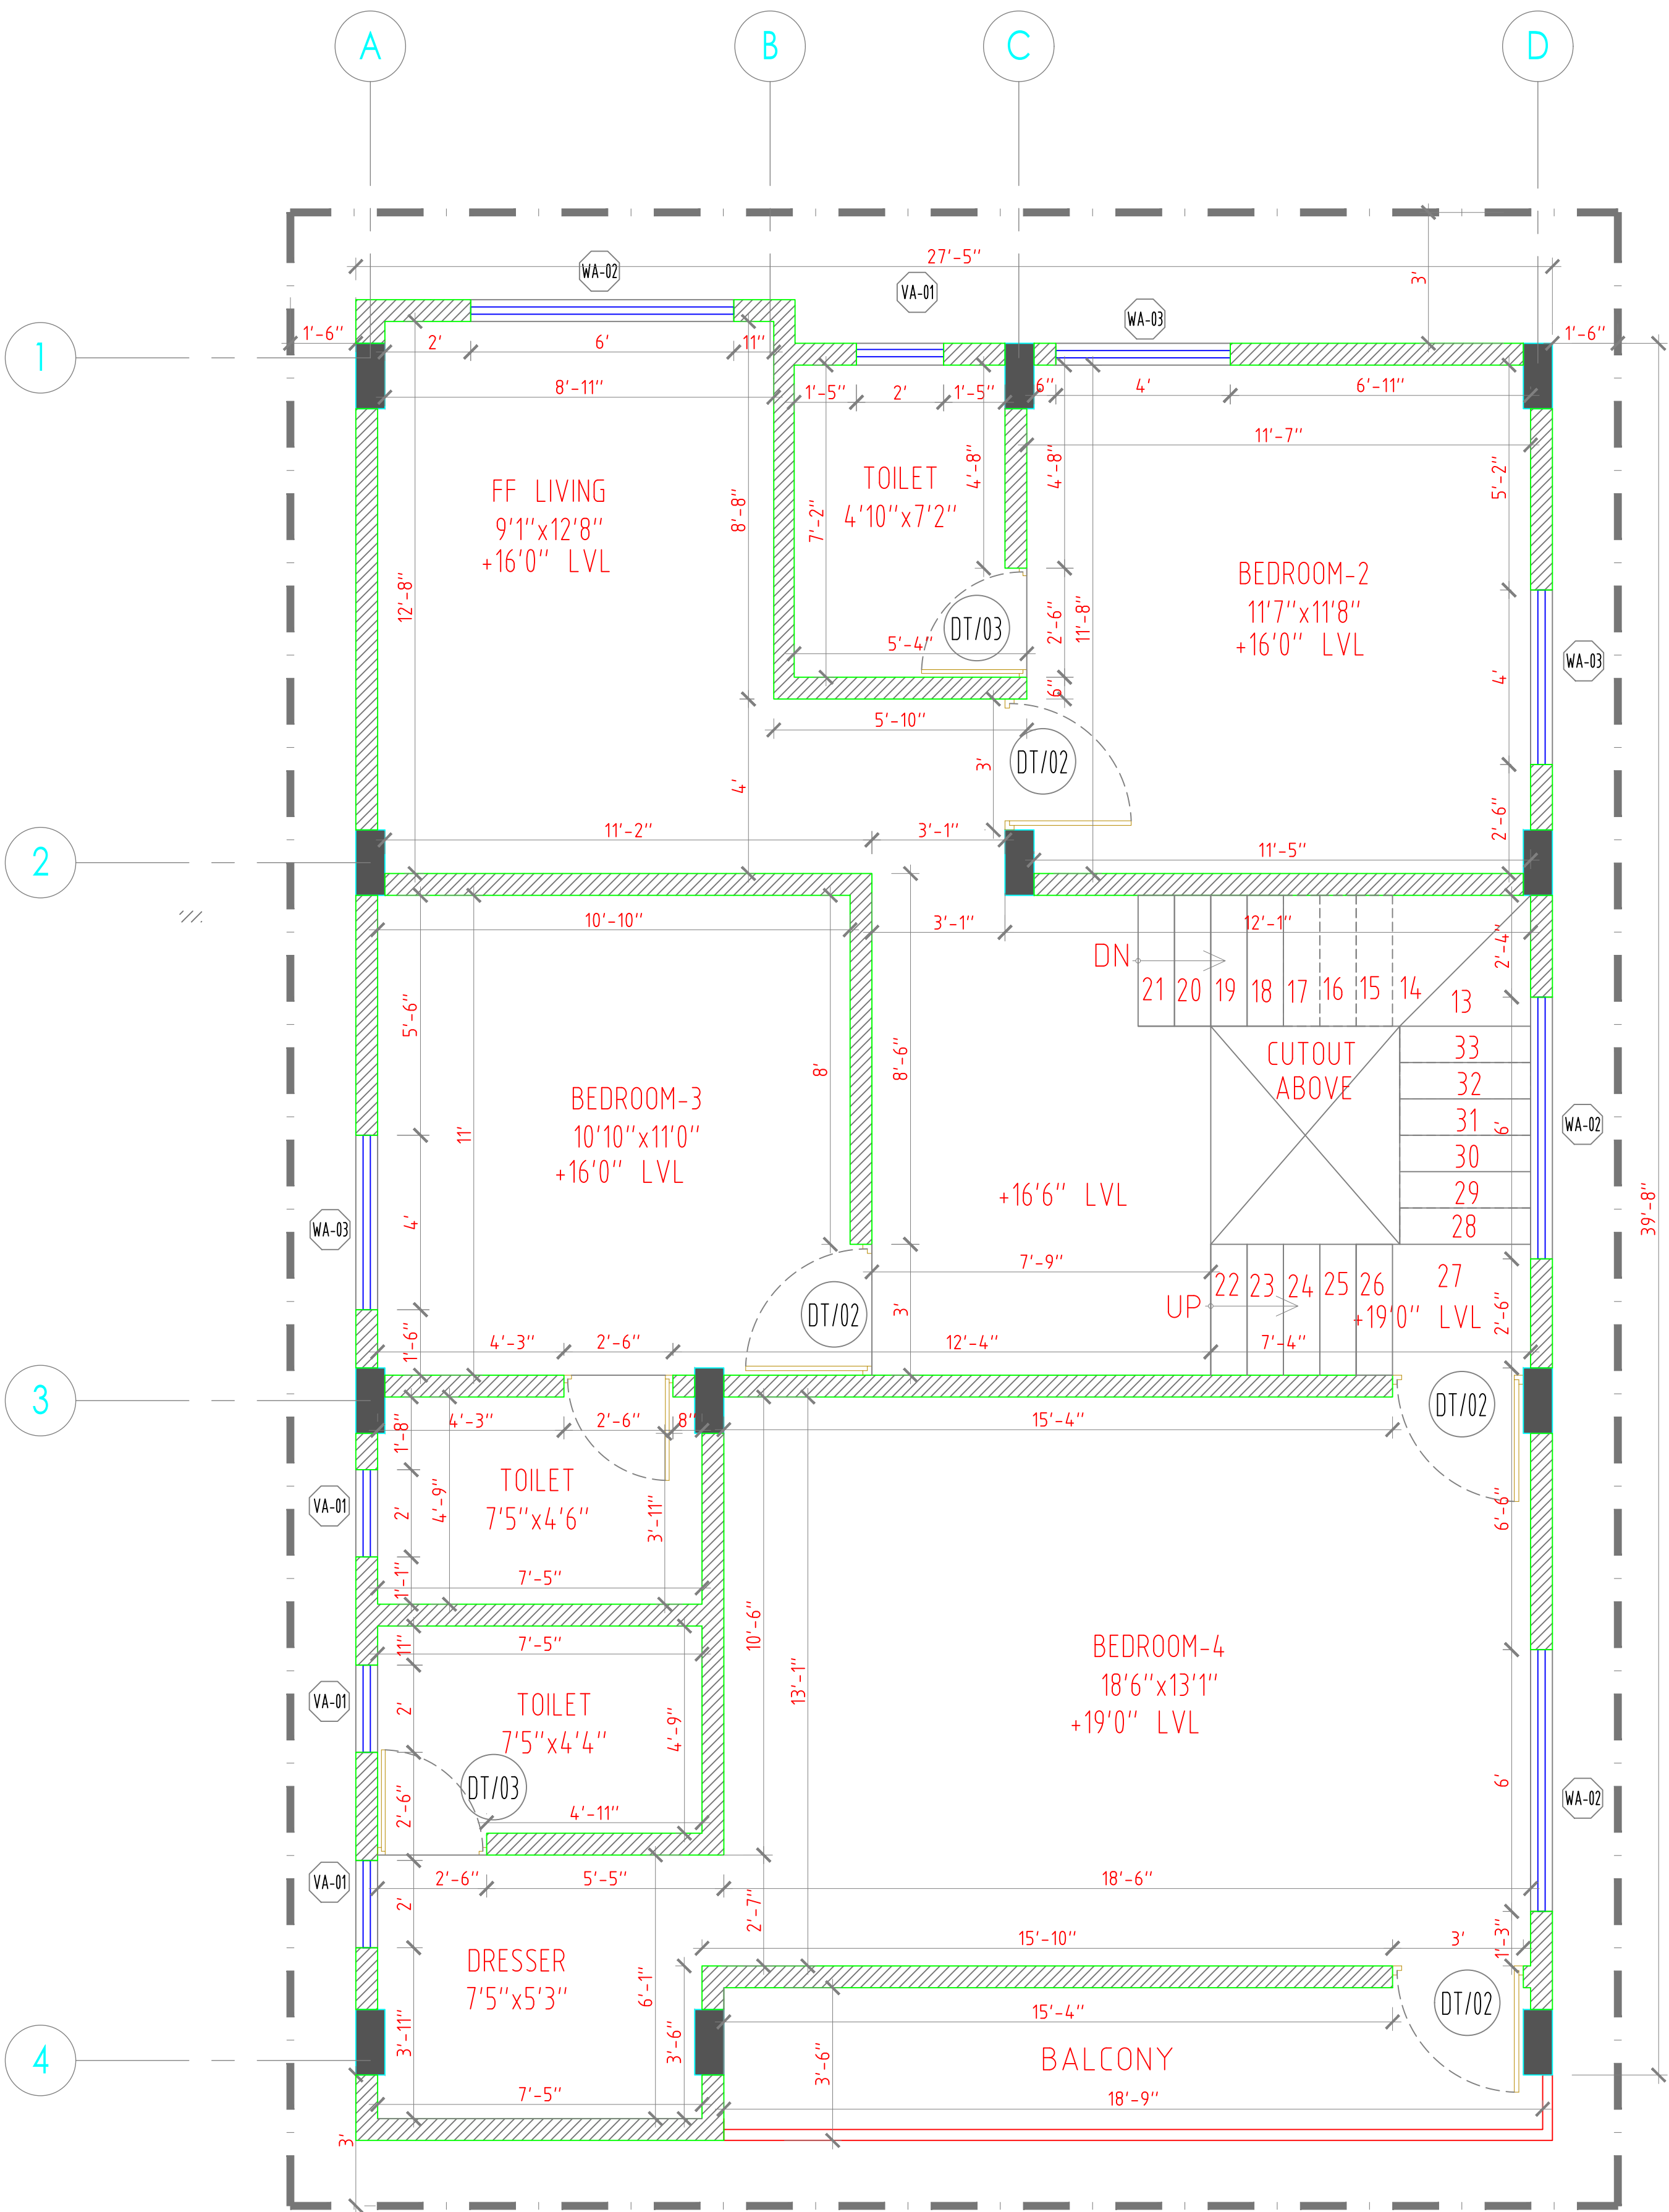


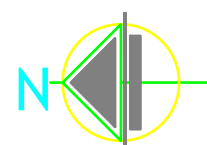

FIRST FLOOR PLAN 01

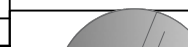

PROJECTS DETAILS :-		CLIENT DETAILS :-		AREA STATEMENT :-		PROJECT TITLE :-		DATE OF SUBMISSION :-		NORTH :-		FROM THE LEGAL TEAM		PARTNER ARCHITECTS :-		OPENING SCHEDULE										Design By :-	
Proposed Residential Villa G+2.		Mr. Narayan				First Floor Plan GFC		07/06/2026				THE ABOVE DRAWING IS THE SOLE PROPERTY OF THE ARCHITECTS AND SHOULD NOT BE PUBLISHED OR USED OTHER WISE WITHOUT THE PRIOR CONSENT OF THE ARCHITECTS.		DSIGN CREW LLP		<table><tr><th></th><th></th><th>SIZE</th><th>SILL</th><th>LINTEL</th><th>NOS</th></tr><tr><td>DT/01</td><td>DOOR</td><td>3'6"x8'0"</td><td>FFL</td><td>7'0"</td><td>1 NOS</td></tr><tr><td>DT/02</td><td>DOOR</td><td>3'0"x8'0"</td><td>FFL</td><td>7'0"</td><td>7 NOS</td></tr><tr><td>DT/03</td><td>DOOR</td><td>2'6"x8'0"</td><td>FFL</td><td>7'0"</td><td>6 NOS</td></tr><tr><td>BD/01</td><td>DOOR</td><td>2'6"x8'0"</td><td>FFL</td><td>7'0"</td><td>2 NOS</td></tr><tr><td>WA-01</td><td>WINDOW</td><td>8'0"x7'0"</td><td>1"</td><td>7'0"</td><td>2 NOS</td></tr><tr><td>WA-02</td><td>WINDOW</td><td>6'0"x5'6"</td><td>2"</td><td>7'0"</td><td>7 NOS</td></tr><tr><td>WA-03</td><td>WINDOW</td><td>4'0"x5'6"</td><td>2"</td><td>7'0"</td><td>8 NOS</td></tr><tr><td>VA-01</td><td>VENTILATOR</td><td>2'0"x2'0"</td><td>6"</td><td>7'0"</td><td>7 NOS</td></tr></table>												SIZE	SILL	LINTEL	NOS	DT/01	DOOR	3'6"x8'0"	FFL	7'0"	1 NOS	DT/02	DOOR	3'0"x8'0"	FFL	7'0"	7 NOS	DT/03	DOOR	2'6"x8'0"	FFL	7'0"	6 NOS	BD/01	DOOR	2'6"x8'0"	FFL	7'0"	2 NOS	WA-01	WINDOW	8'0"x7'0"	1"	7'0"	2 NOS	WA-02	WINDOW	6'0"x5'6"	2"	7'0"	7 NOS	WA-03	WINDOW	4'0"x5'6"	2"	7'0"	8 NOS	VA-01	VENTILATOR	2'0"x2'0"	6"	7'0"	7 NOS	 AR.VIVEKANANDAN D arch VISHAL ARCHITECTS Architects and Interiors	
								SIZE	SILL	LINTEL	NOS	
		DT/01	DOOR					3'6"x8'0"	FFL	7'0"	1 NOS	
DT/02	DOOR	3'0"x8'0"	FFL	7'0"	7 NOS	
DT/03	DOOR	2'6"x8'0"	FFL	7'0"	6 NOS	
BD/01	DOOR	2'6"x8'0"	FFL	7'0"	2 NOS	
WA-01	WINDOW	8'0"x7'0"	1"	7'0"	2 NOS	
WA-02	WINDOW	6'0"x5'6"	2"	7'0"	7 NOS	
WA-03	WINDOW	4'0"x5'6"	2"	7'0"	8 NOS	
VA-01	VENTILATOR	2'0"x2'0"	6"	7'0"	7 NOS	
SITE ADDRESS :-	
Prestige Great Acres	
								REVISION NUMBER :-		SCALE :-		POWERED THROUGH :-		Jsw ONE HOMES												PH : 6381358459 E-mail: vishalarchitects307@gmail.com	
								R No. R2		1:100	