



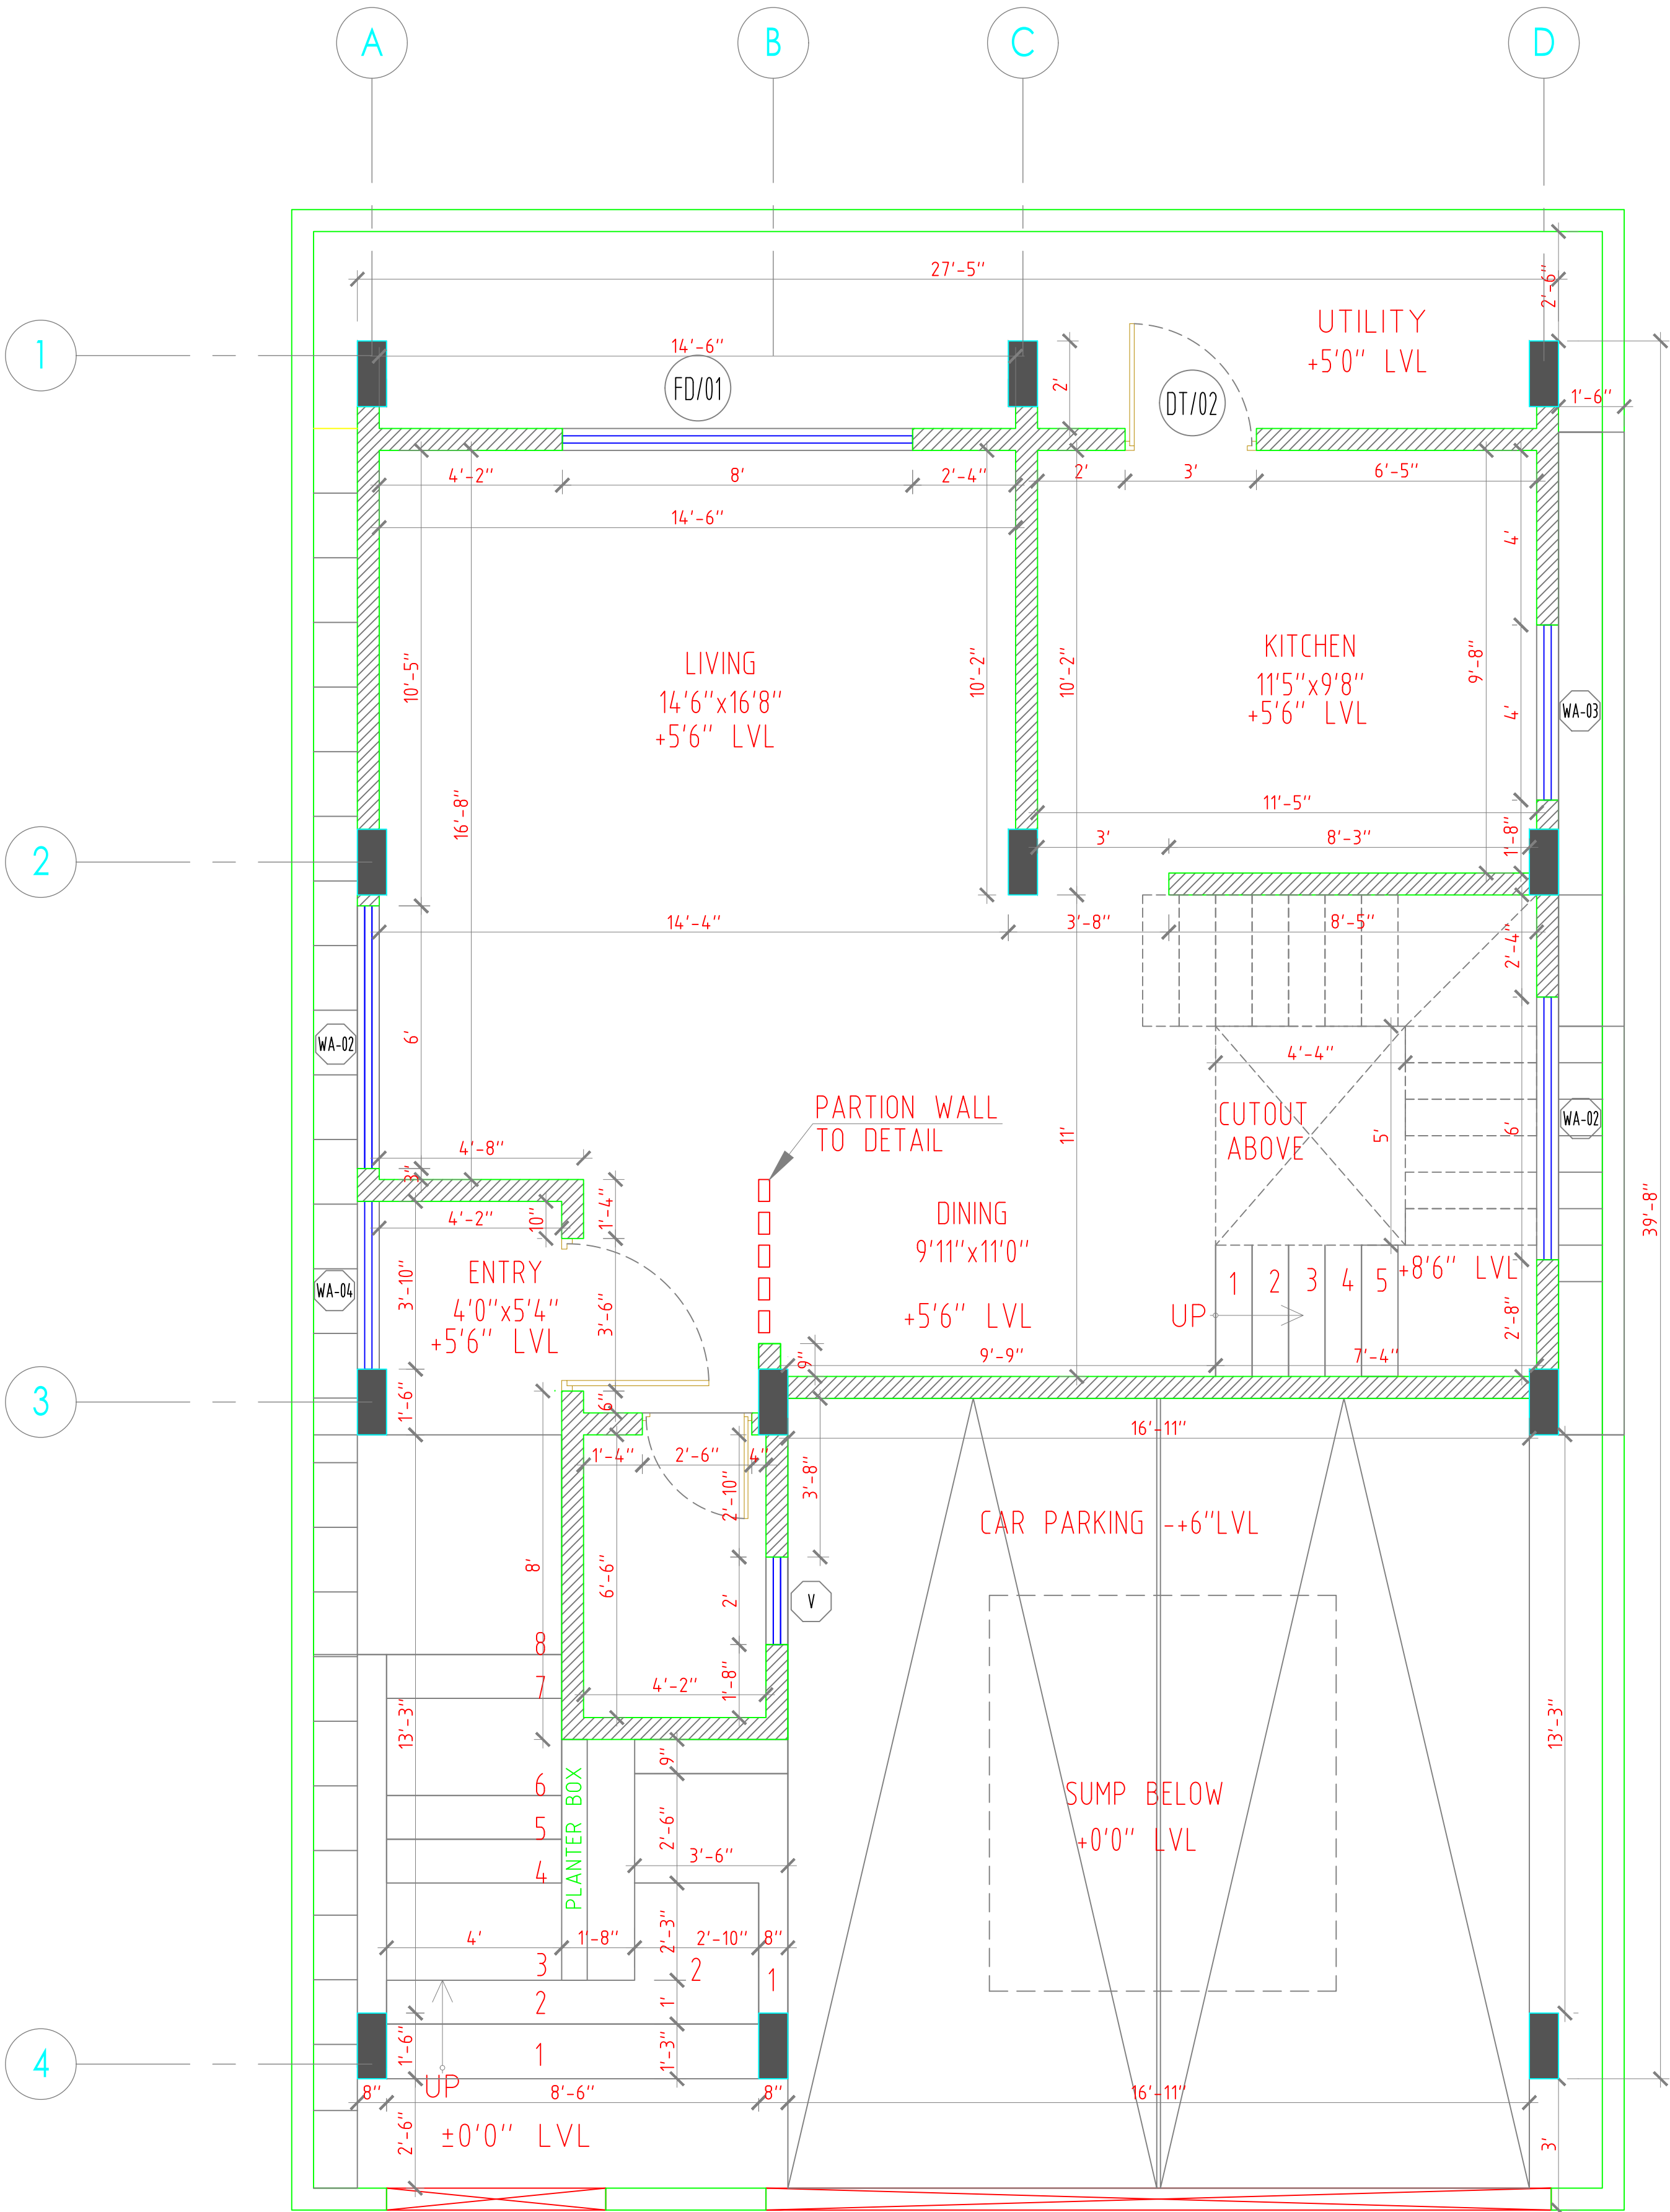

GATE GATE

GROUND FLOOR PLAN - LEVEL 1 01

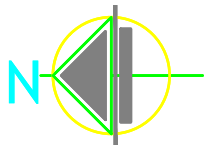

PROJECTS DETAILS :-		CLIENT DETAILS :-		AREA STATEMENT :-		PROJECT TITLE :-		DATE OF SUBMISSION :-		NORTH :-		FROM THE LEGAL TEAM		PARTNER ARCHITECTS :-		OPENING SCHEDULE										Design By :-	
Proposed Residential Villa G+2.		Mr. Narayan				Ground Floor Plan GFC		07/06/2026				THE ABOVE DRAWING IS THE SOLE PROPERTY OF THE ARCHITECTS AND SHOULD NOT BE PUBLISHED OR USED OTHER WISE WITHOUT THE PRIOR CONSENT OF THE ARCHITECTS.		DSIGN CREW LLP		DT/01 DOOR 3'6"x8'0" FFL 7'0" 1 NOS										 AR.VIVEKANANDAN 6 arch VISHAL ARCHITECTS Architects and Interiors	
								REVISION NUMBER :-		SCALE :-						DT/02 DOOR 3'0"x8'0" FFL 7'0" 7 NOS											
		R No. R2						1:100		DT/03 DOOR 2'6"x8'0" FFL 7'0" 6 NOS																	
										BD/01 DOOR 2'6"x8'0" FFL 7'0" 2 NOS																	
										WA-01 WINDOW 8'0"x7'0" 1'0" 7'0" 2 NOS																	
										WA-02 WINDOW 6'0"x5'6" 2'6" 7'0" 7 NOS																	
SITE ADDRESS :-																WA-03 WINDOW 4'0"x5'6" 2'6" 7'0" 8 NOS											
Prestige Great Acres																		VA-01 VENTILATOR 2'0"x2'0" 6'0" 7'0" 7 NOS									
																						PH : 6381358459					
																						E-mail: vishalarchitects307@gmail.com					