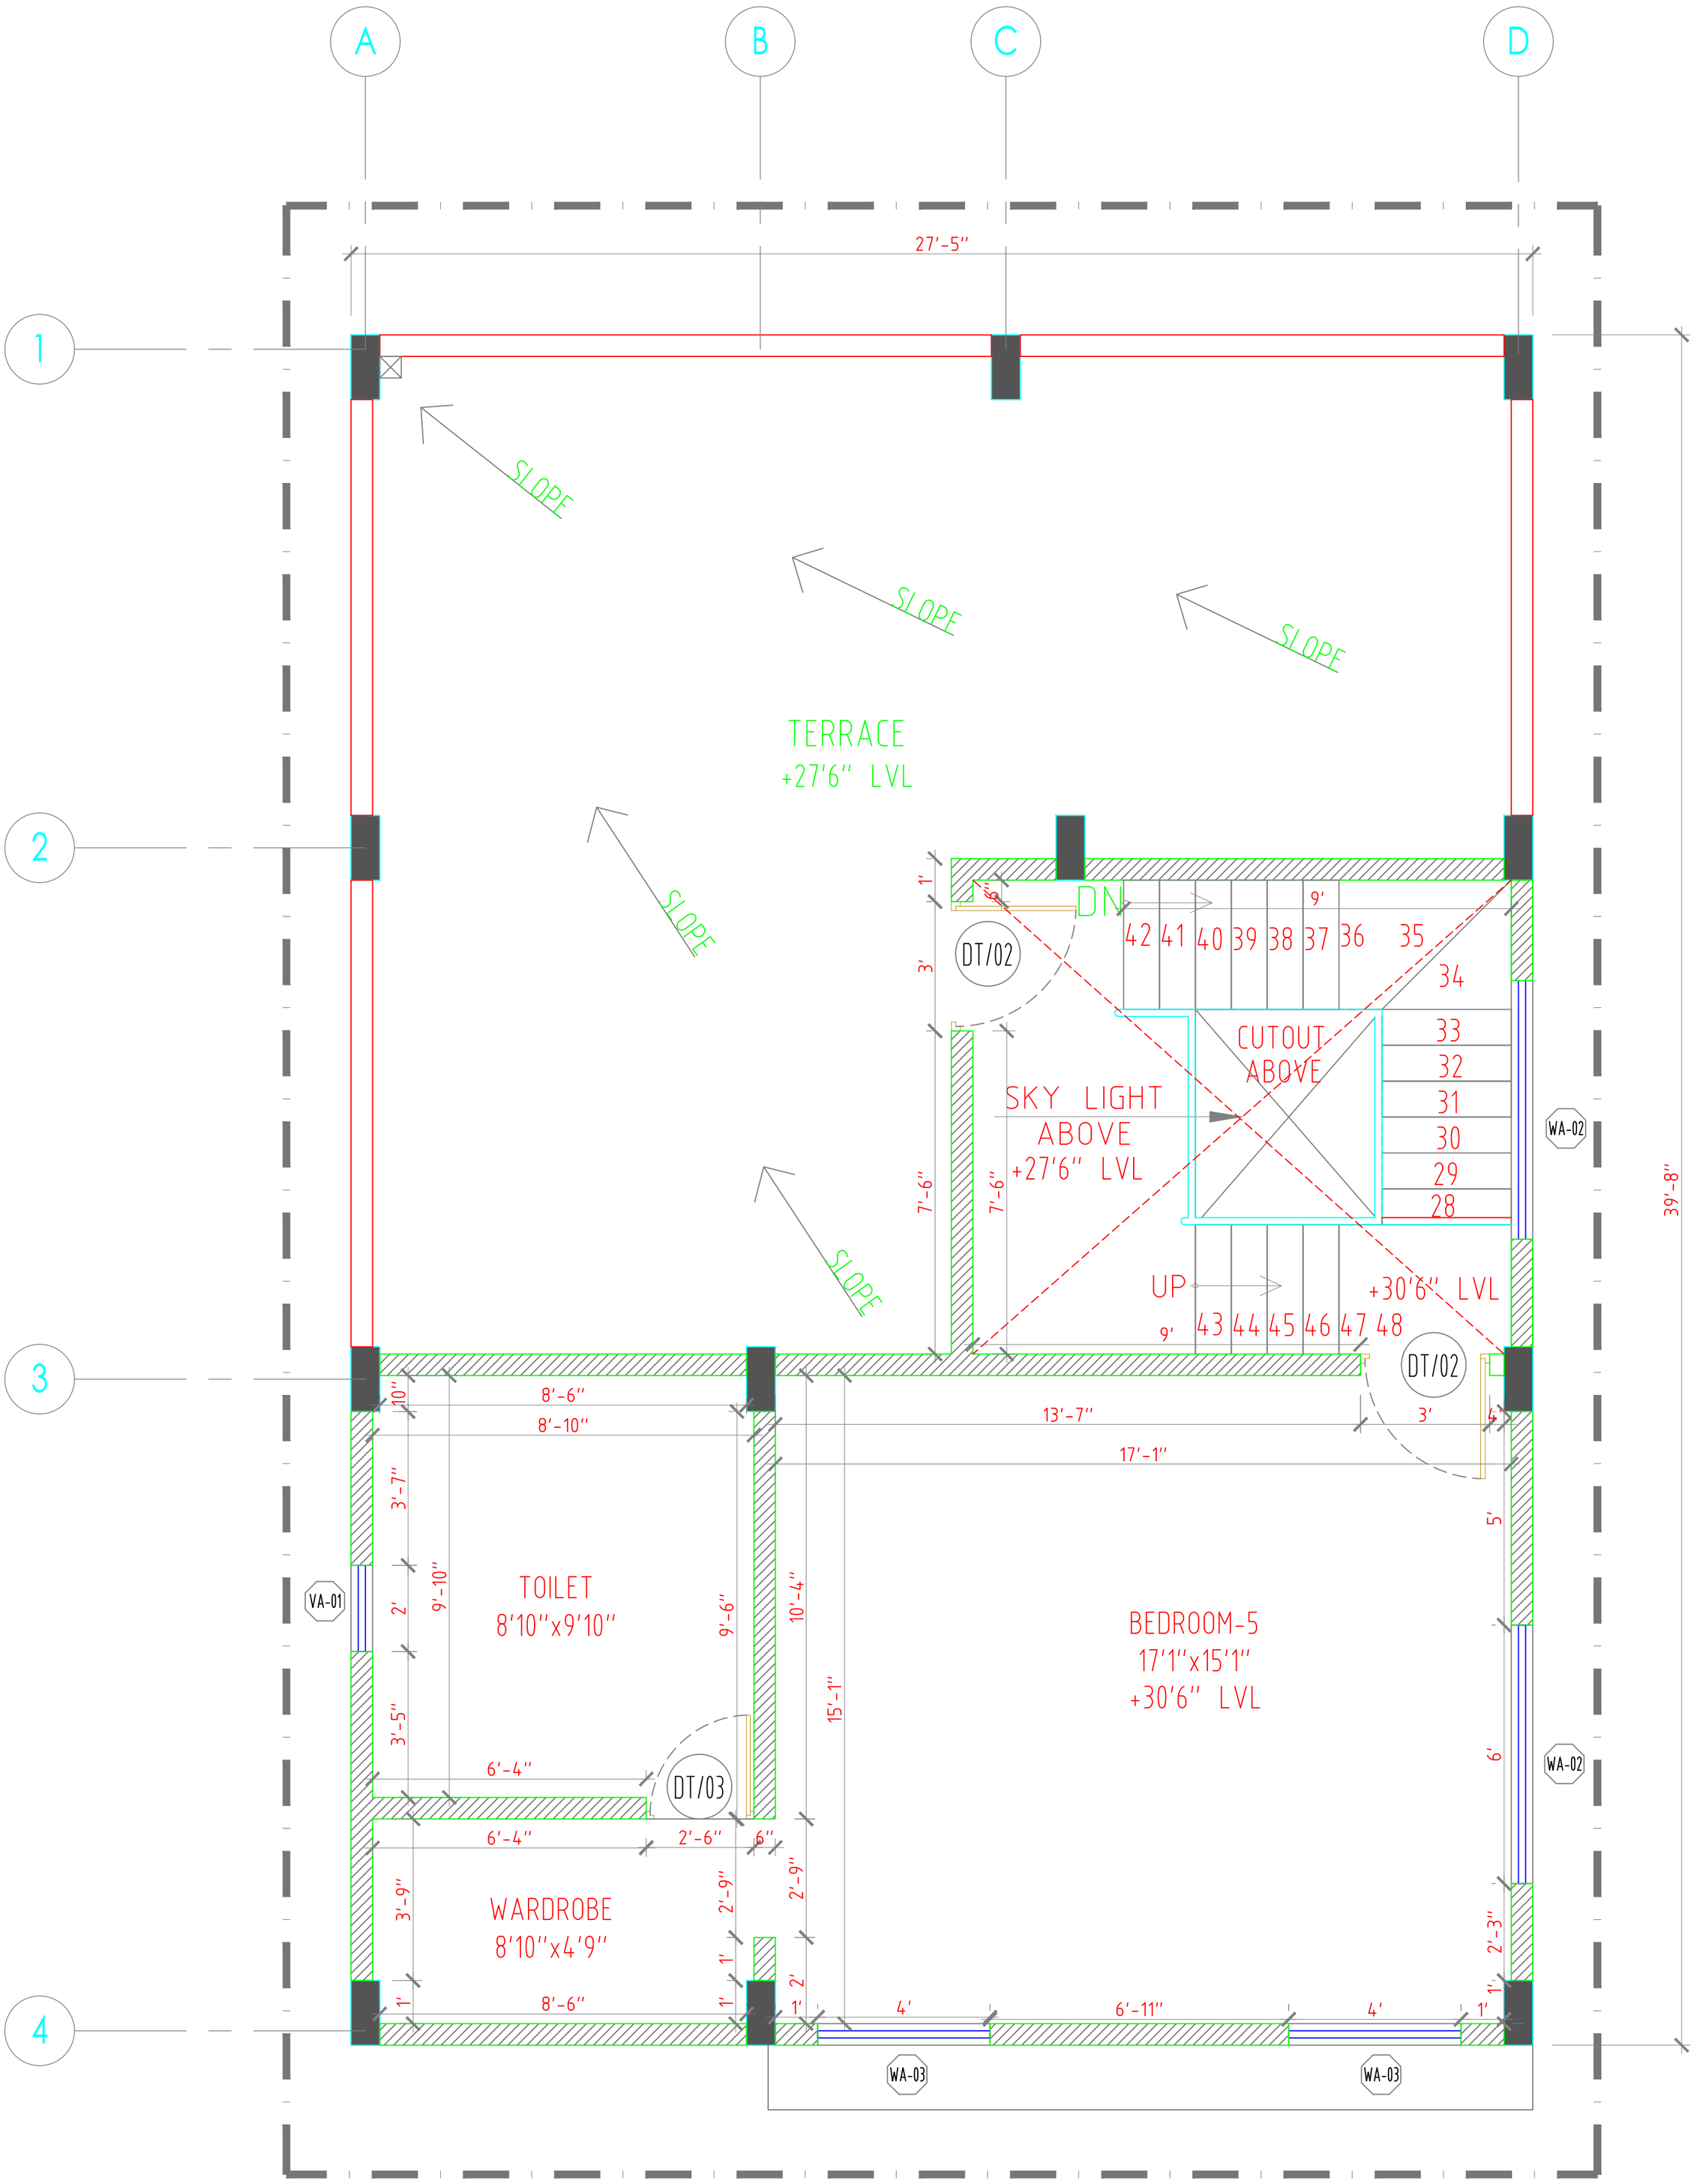


SECOND FLOOR PLAN 01

N

PROJECTS DETAILS :-	CLIENT DETAILS :-	AREA STATEMENT :-	PROJECT TITLE :-	DATE OF SUBMISSION :-	NORTH :-	FROM THE LEGAL TEAM	PARTNER ARCHITECTS :-
Proposed Residential Villa G+2.	Mr. Narayan SITE ADDRESS :- Prestige Great Acres		Second Floor Plan GFC	07/06/2026 REVISION NUMBER :- R No. R2	E N S W SCALE :- 1:100	THE ABOVE DRAWING IS THE SOLE PROPERTY OF THE ARCHITECTS AND SHOULD NOT BE PUBLISHED OR USED OTHER WISE WITHOUT THE PRIOR CONSENT OF THE ARCHITECTS.	DSIGN CREW LLP POWERED THROUGH :- JSW ONE HOMES

	OPENING SCHEDULE				
		SIZE	SILL	LINTEL	NOS
DT/01	DOOR	3'6"x8'0"	FFL	7'0"	1 NOS
DT/02	DOOR	3'0"x8'0"	FFL	7'0"	7 NOS
DT/03	DOOR	2'6"x8'0"	FFL	7'0"	6 NOS
BD/01	DOOR	2'6"x8'0"	FFL	7'0"	2 NOS
WA-01	WINDOW	8'0"x7'0"	1'0"	7'0"	2 NOS
WA-02	WINDOW	6'0"x5'6"	2'6"	7'0"	7 NOS
WA-03	WINDOW	4'0"x5'6"	2'6"	7'0"	8 NOS
VA-01	VENTILATOR	2'0"x2'0"	6'0"	7'0"	7 NOS

Design By :-
AR.VIVEKANANDAN
D.arch
VISHAL ARCHITECTS
Architects and Interiors
PH : 6381358459
E-mail- vishalarchitects307@gmail.com